

站点分级台账

分级依据：官方公告四至（北至北五环路、东至京藏高速与学院路、南至西直门外大街、西至万泉河路与大钟寺东路），对每座车站逐一做点面判定。站位取自 OpenStreetMap，属概念定位；出入口与步行网络须以实测数据替换。

总体设计范围内 · 逐站详细设计（7座）

学知园 27 · 众智园AI自主创新加速区

众智园北端研发接驳门户

现状问题：站点位于重点区内部，但东侧京藏高速与北五环形成双重切割，园区与站点间缺连续步行面。

近期动作：跨京藏高速人行天桥或地道加宽，取消绕行；站口 200m 内连续无障碍步道与雨棚；园区围墙开口，形成站到园直连

六道口 15/27 · 近北京AI原点社区 684m

原点社区北门户与校城缝合点

现状问题：紧邻 AI 原点社区边界（684m）但被学院路主干与校园围墙夹持，过街等待长。

近期动作：学院路平交口行人相位优先，压缩等待；校园东南角围墙开口接入站口；站口自行车停放正规化，清理占道

学院桥 27 · 北京AI原点社区

AI 原点社区核心站城复合核

现状问题：站点落在重点区内，但立交桥区人车混行、导视缺失，桥下空间闲置。

近期动作：立交桥下空间改造为有照明的步行连廊与公共活动场；四向连续过街与统一导视；径向绿廊穿透，替代封闭绿带

西土城 10/27 · 近北京AI原点社区 958m

研学与生活混合的中段站

现状问题：距原点社区 958m，处于两重点区之间的接续段，沿线业态单一、夜间冷清。

近期动作：沿站步行街段首层业态激活，避免纯办公；补齐夜间照明与连续遮阴；接入南北慢行脊

蓟门桥 27 · 近大钟寺AI产业聚集区 1828m

南段承接站与绿脊节点

现状问题：距第三重点区 1.8km，位于慢行脊中段，主干路切断东西向步行联系。

近期动作：东西向过街加密，缩短绕行；绿脊在此段连通，不做封闭隔离带；站口公共休憩与遮阴

北京北 S5 · 大钟寺AI产业聚集区

京张遗产门户与市郊铁路接口（S5）

现状问题：位于第三重点区临时 polygon 内，是市郊铁路而非地铁站；与西直门地铁换乘步行距离长、指引弱。

近期动作：北京北—西直门换乘通道连续化与统一导视；京张遗址公园在此设主入口；站前广场机动车与步行分离

西直门 13/2/4 · 近大钟寺AI产业聚集区 531m

南端城市级换乘锚点（2/4/13 号线）

现状问题：三线换乘且紧邻研究范围南界，站城被西直门外大街与立交切割，属高强度既有建成区。

近期动作：换乘导视与步行连续性优先，不做大拆大建；西直门外大街过街与非机动车路权改善；既有社区以更新为主，保留小商户

统筹研究范围内 · 廊道与接驳层级（14座）

林萃桥 8 北端接驳，8 号线换乘进入研究范围

北沙滩 15 东北向接驳，15 号线

清华东路西口 15 校城接驳，15 号线

五道口 13 高校就业与生活锚点，13 号线（距原点社区 879m）

知春路 10/13 10/13 换乘，西向就业接驳

知春里 10 10 号线，居住接驳

牡丹园 10/19 10/19 换乘，东侧居住接驳

北太平庄 19 19 号线，南段居住接驳

人民大学 4 4 号线，高校与就业接驳


大钟寺 13 13 号线；真实站位在重点区临时 polygon 以北约 1.7km，须以实测站位复核


魏公村 4 4 号线，高校接驳

积水潭 19/2 2/19 换乘，南端城市接驳

国家图书馆 16/4/9 4/9/16 换乘，西南向接驳

新街口 4 4 号线，南端生活接驳

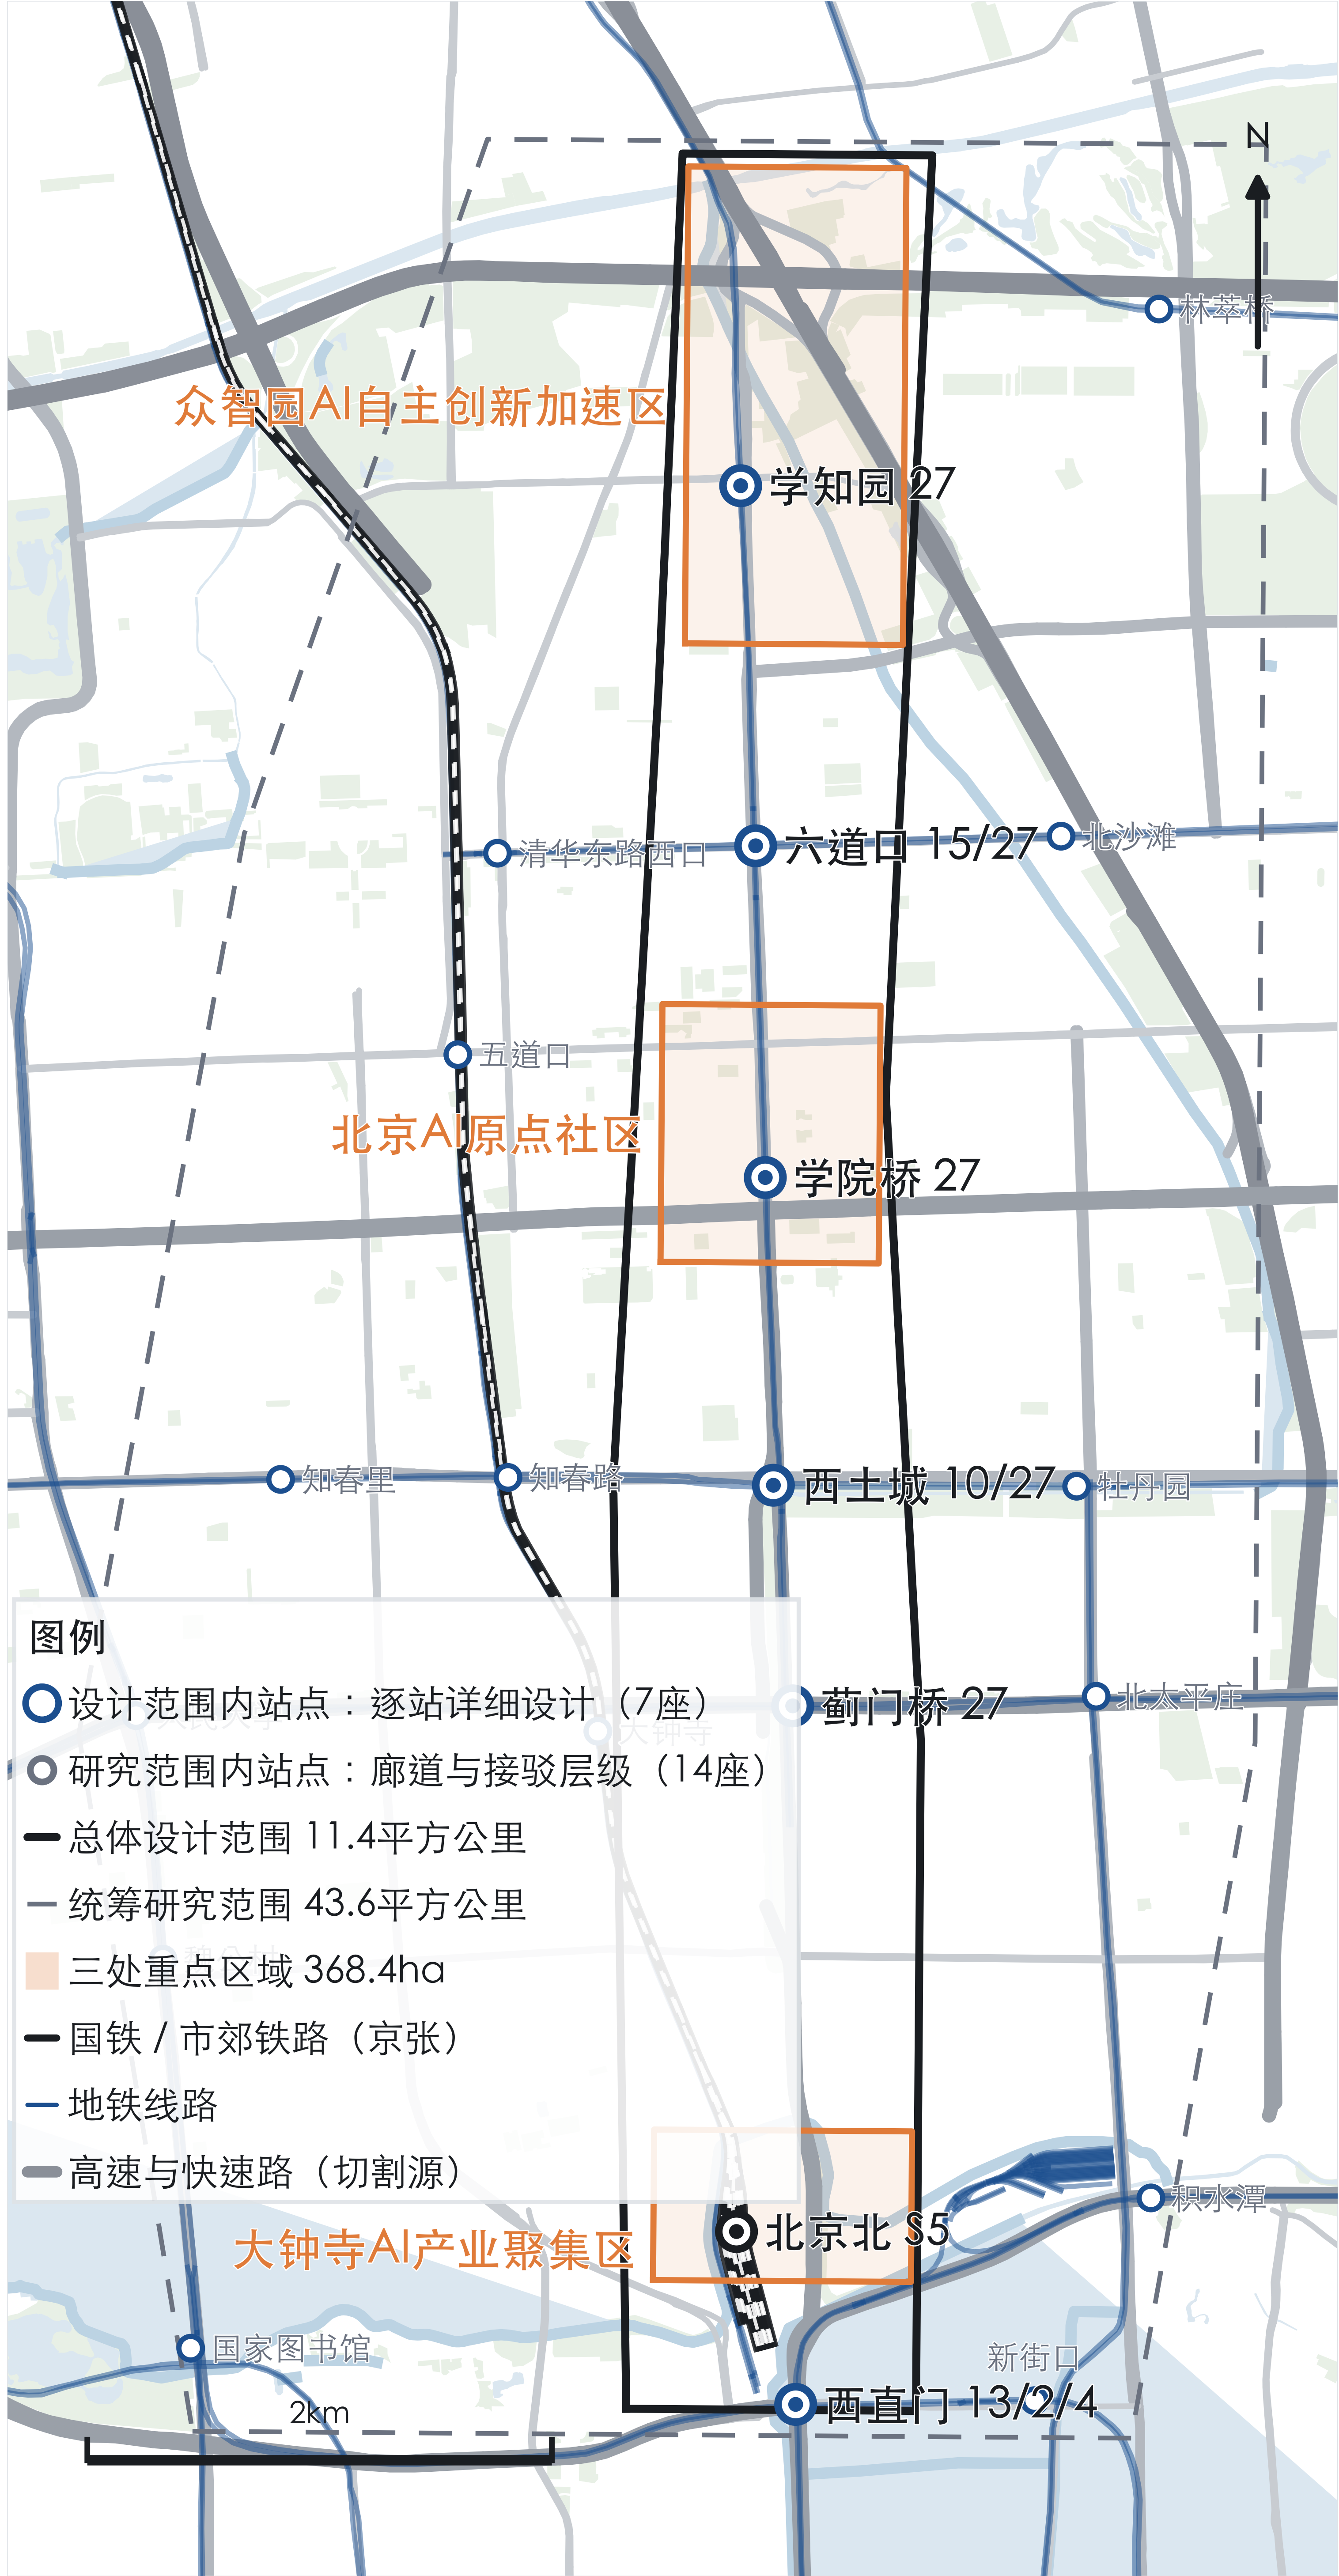

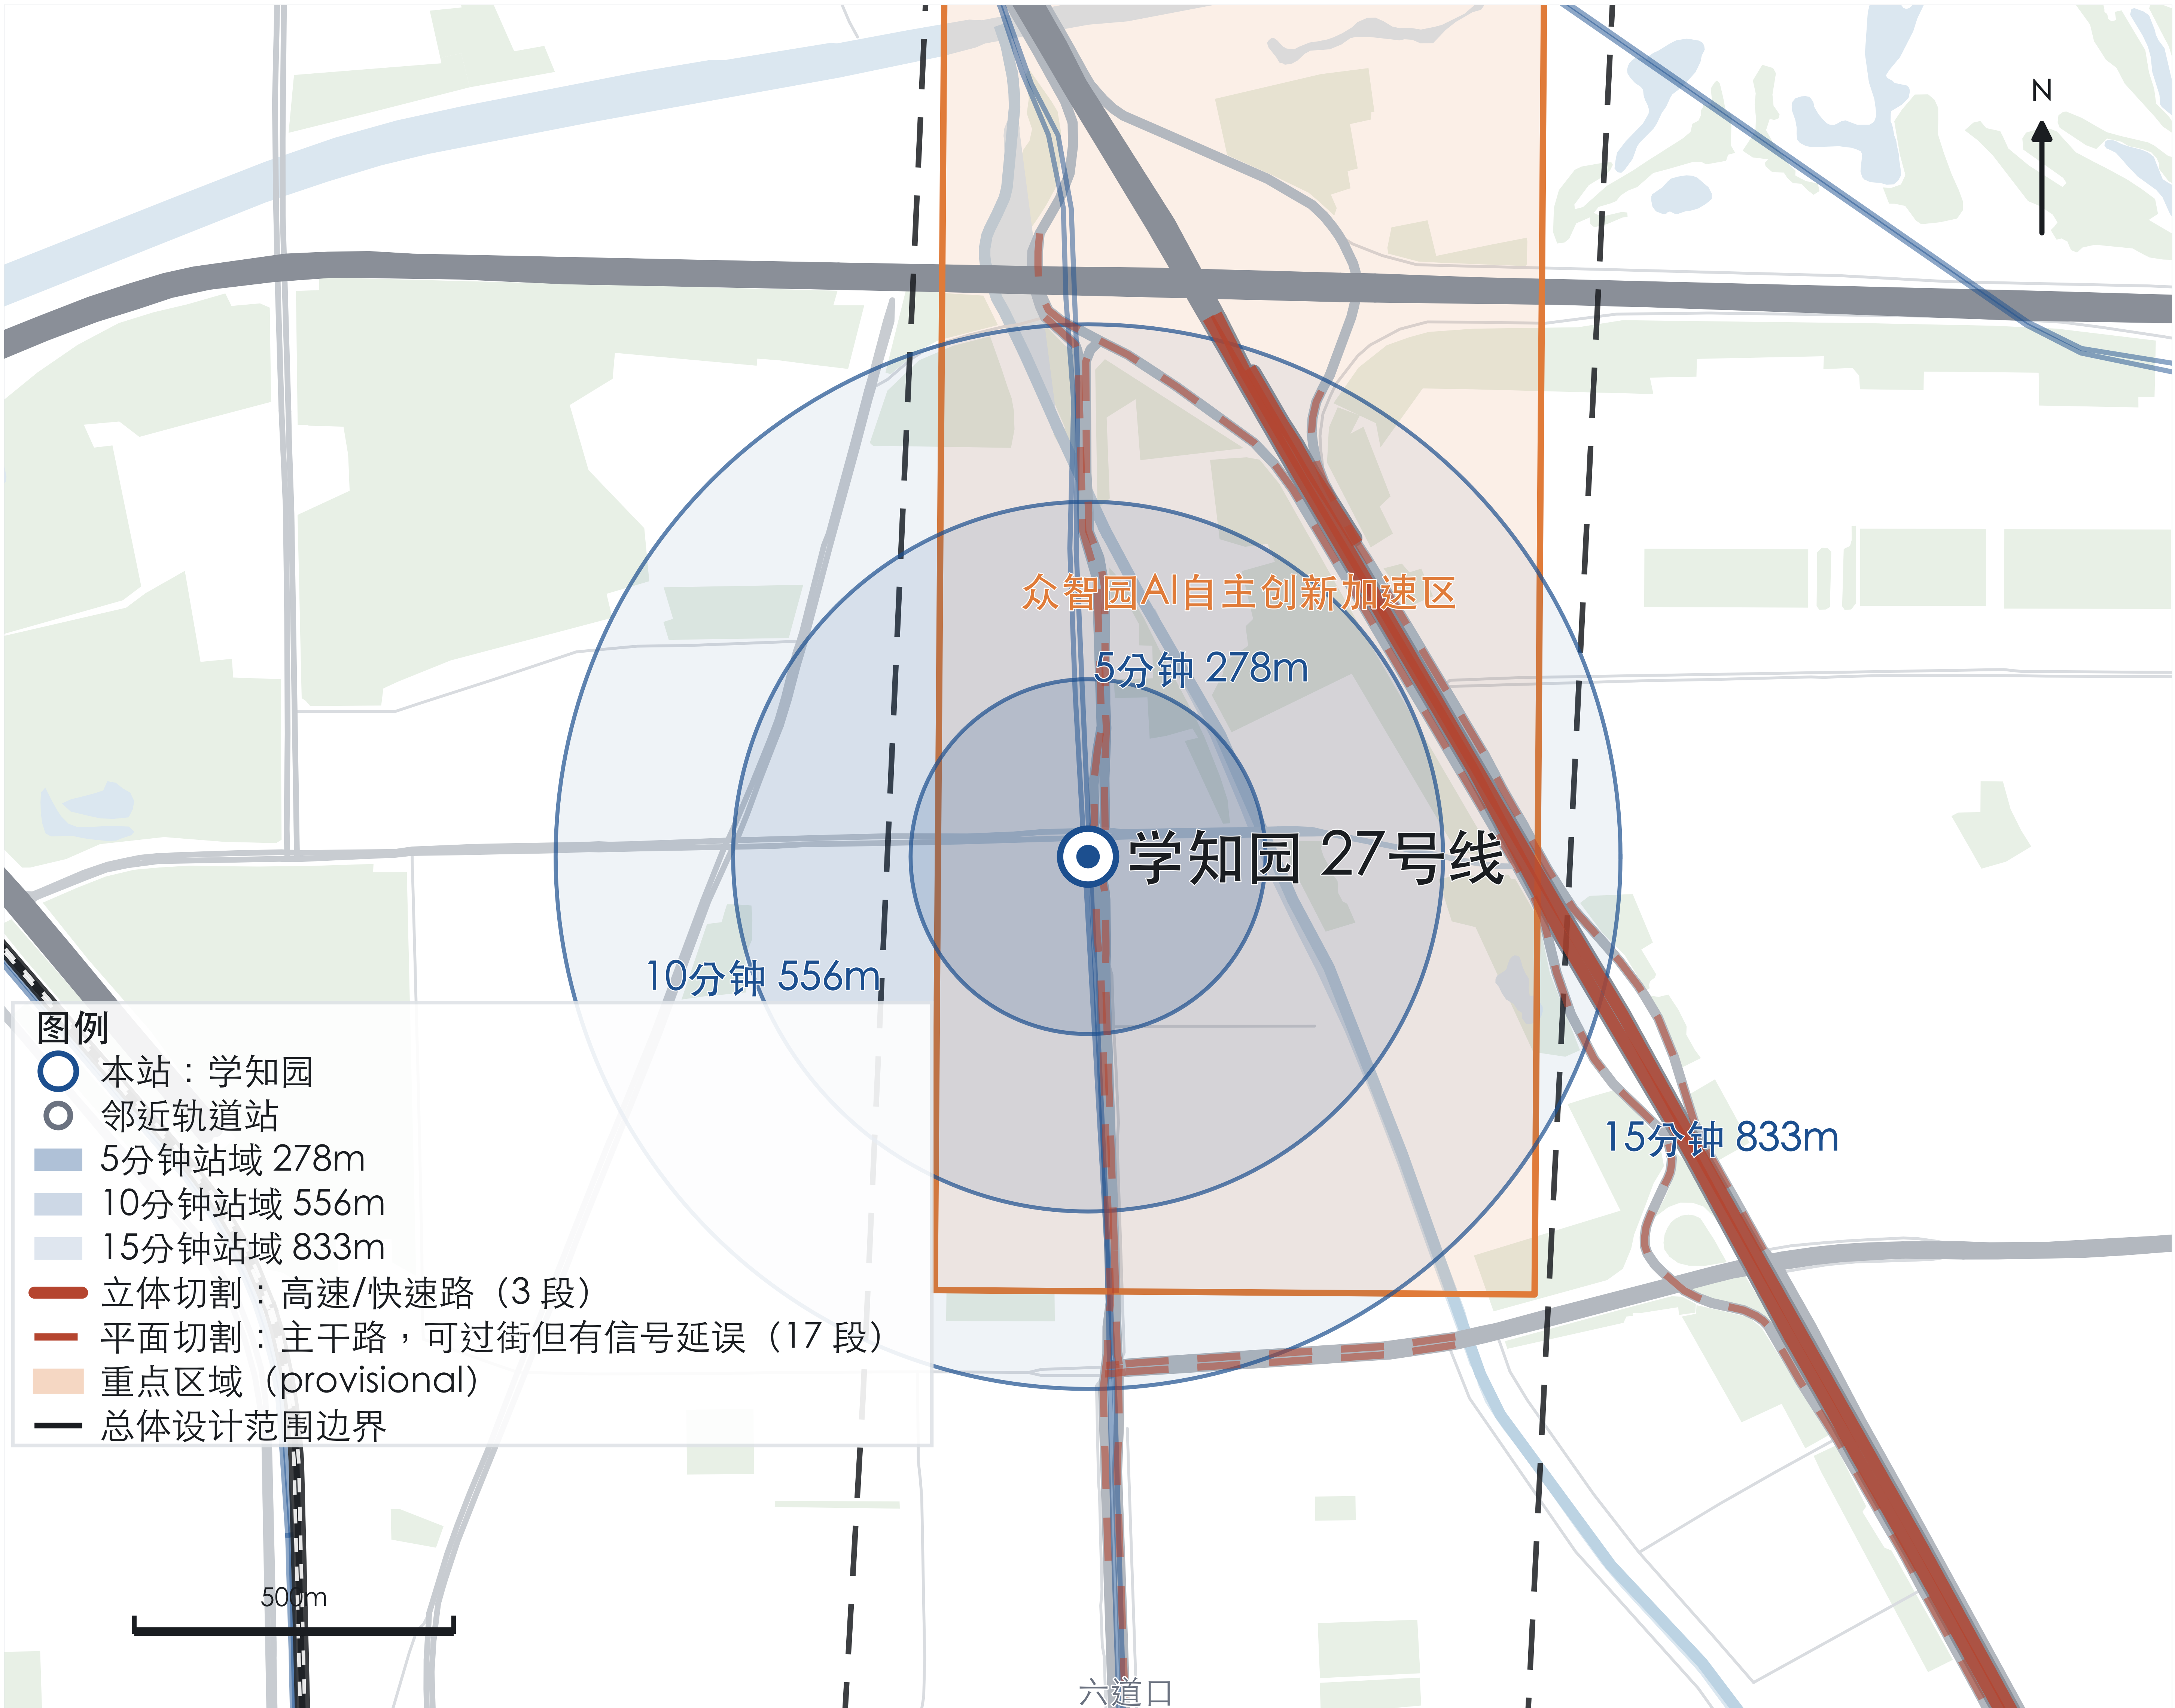

现状诊断

站点位于重点区内部，但东侧京藏高速与北五环形成双重切割，园区与站点间缺连续步行面。

站域口径

站域以车站出入口为原点按步行可达界定，不用车站中心直线半径。半径 = 分钟 × 75 m/min ÷ 1.35 绕行系数，故本站 5 分钟 278m、10 分钟 556m、15 分钟 833m。

切割诊断：立体 3 段 / 平面 17 段

实线为 OSM motorway 与 trunk 等级道路，属立体切割，只能靠桥隧过街，是步行可达的硬断点。虚线为 primary 等级主干路，属平面切割，可过街但受信号周期与路口宽度影响。凡被切割线穿过的圈层为名义可达、实际须绕行或等待，须以实测步行网络与过街点位切除后重算。

待实测

- 高速两侧步行流量与绕行距离
- 园区权属与开口可行性
- 站厅高峰客流

5 分钟核心 · 278m

- 通勤接驳厅
- 早餐与夜间餐饮
- 共享实验与中试展示
- 轮班工作者休息

10 分钟圈 · 556m

- 青年与普通职工租赁住房
- 社区医疗与托育
- 便利商业
- 低速接驳测试道

15 分钟圈 · 833m

以既有社区更新为主，不以拆迁换取形式整齐；补齐普通就业、教育医疗与公交接驳，保留小商户与可承受租金。

密度与混合梯度

出入口周边最高、向外递减，功能混合度随距离下降。此处只给相对关系：官方控规与精确边界未发布，容积率与建筑高度保持 unknown，本图不给具体数值。

近期动作

不依赖大拆建、可先行、可回退：


1. 跨京藏高速人行天桥或地道加宽，取消绕行
2. 站口 200m 内连续无障碍步道与雨棚
3. 园区围墙开口，形成站到园直连

站城一体

出入口、公交站台、非机动车停放、人行系统与建筑首层应在同一标高连续贯通，避免出闸后再上下天桥；非机动车在出入口 50m 内集中停放并清理占道。

本图性质

概念设计建议，非法定规划成果。站位为 OpenStreetMap provisional 数据，实测出入口替换后须复算站域与步行圈；边界为仓库 provisional 数据，非官方红线。

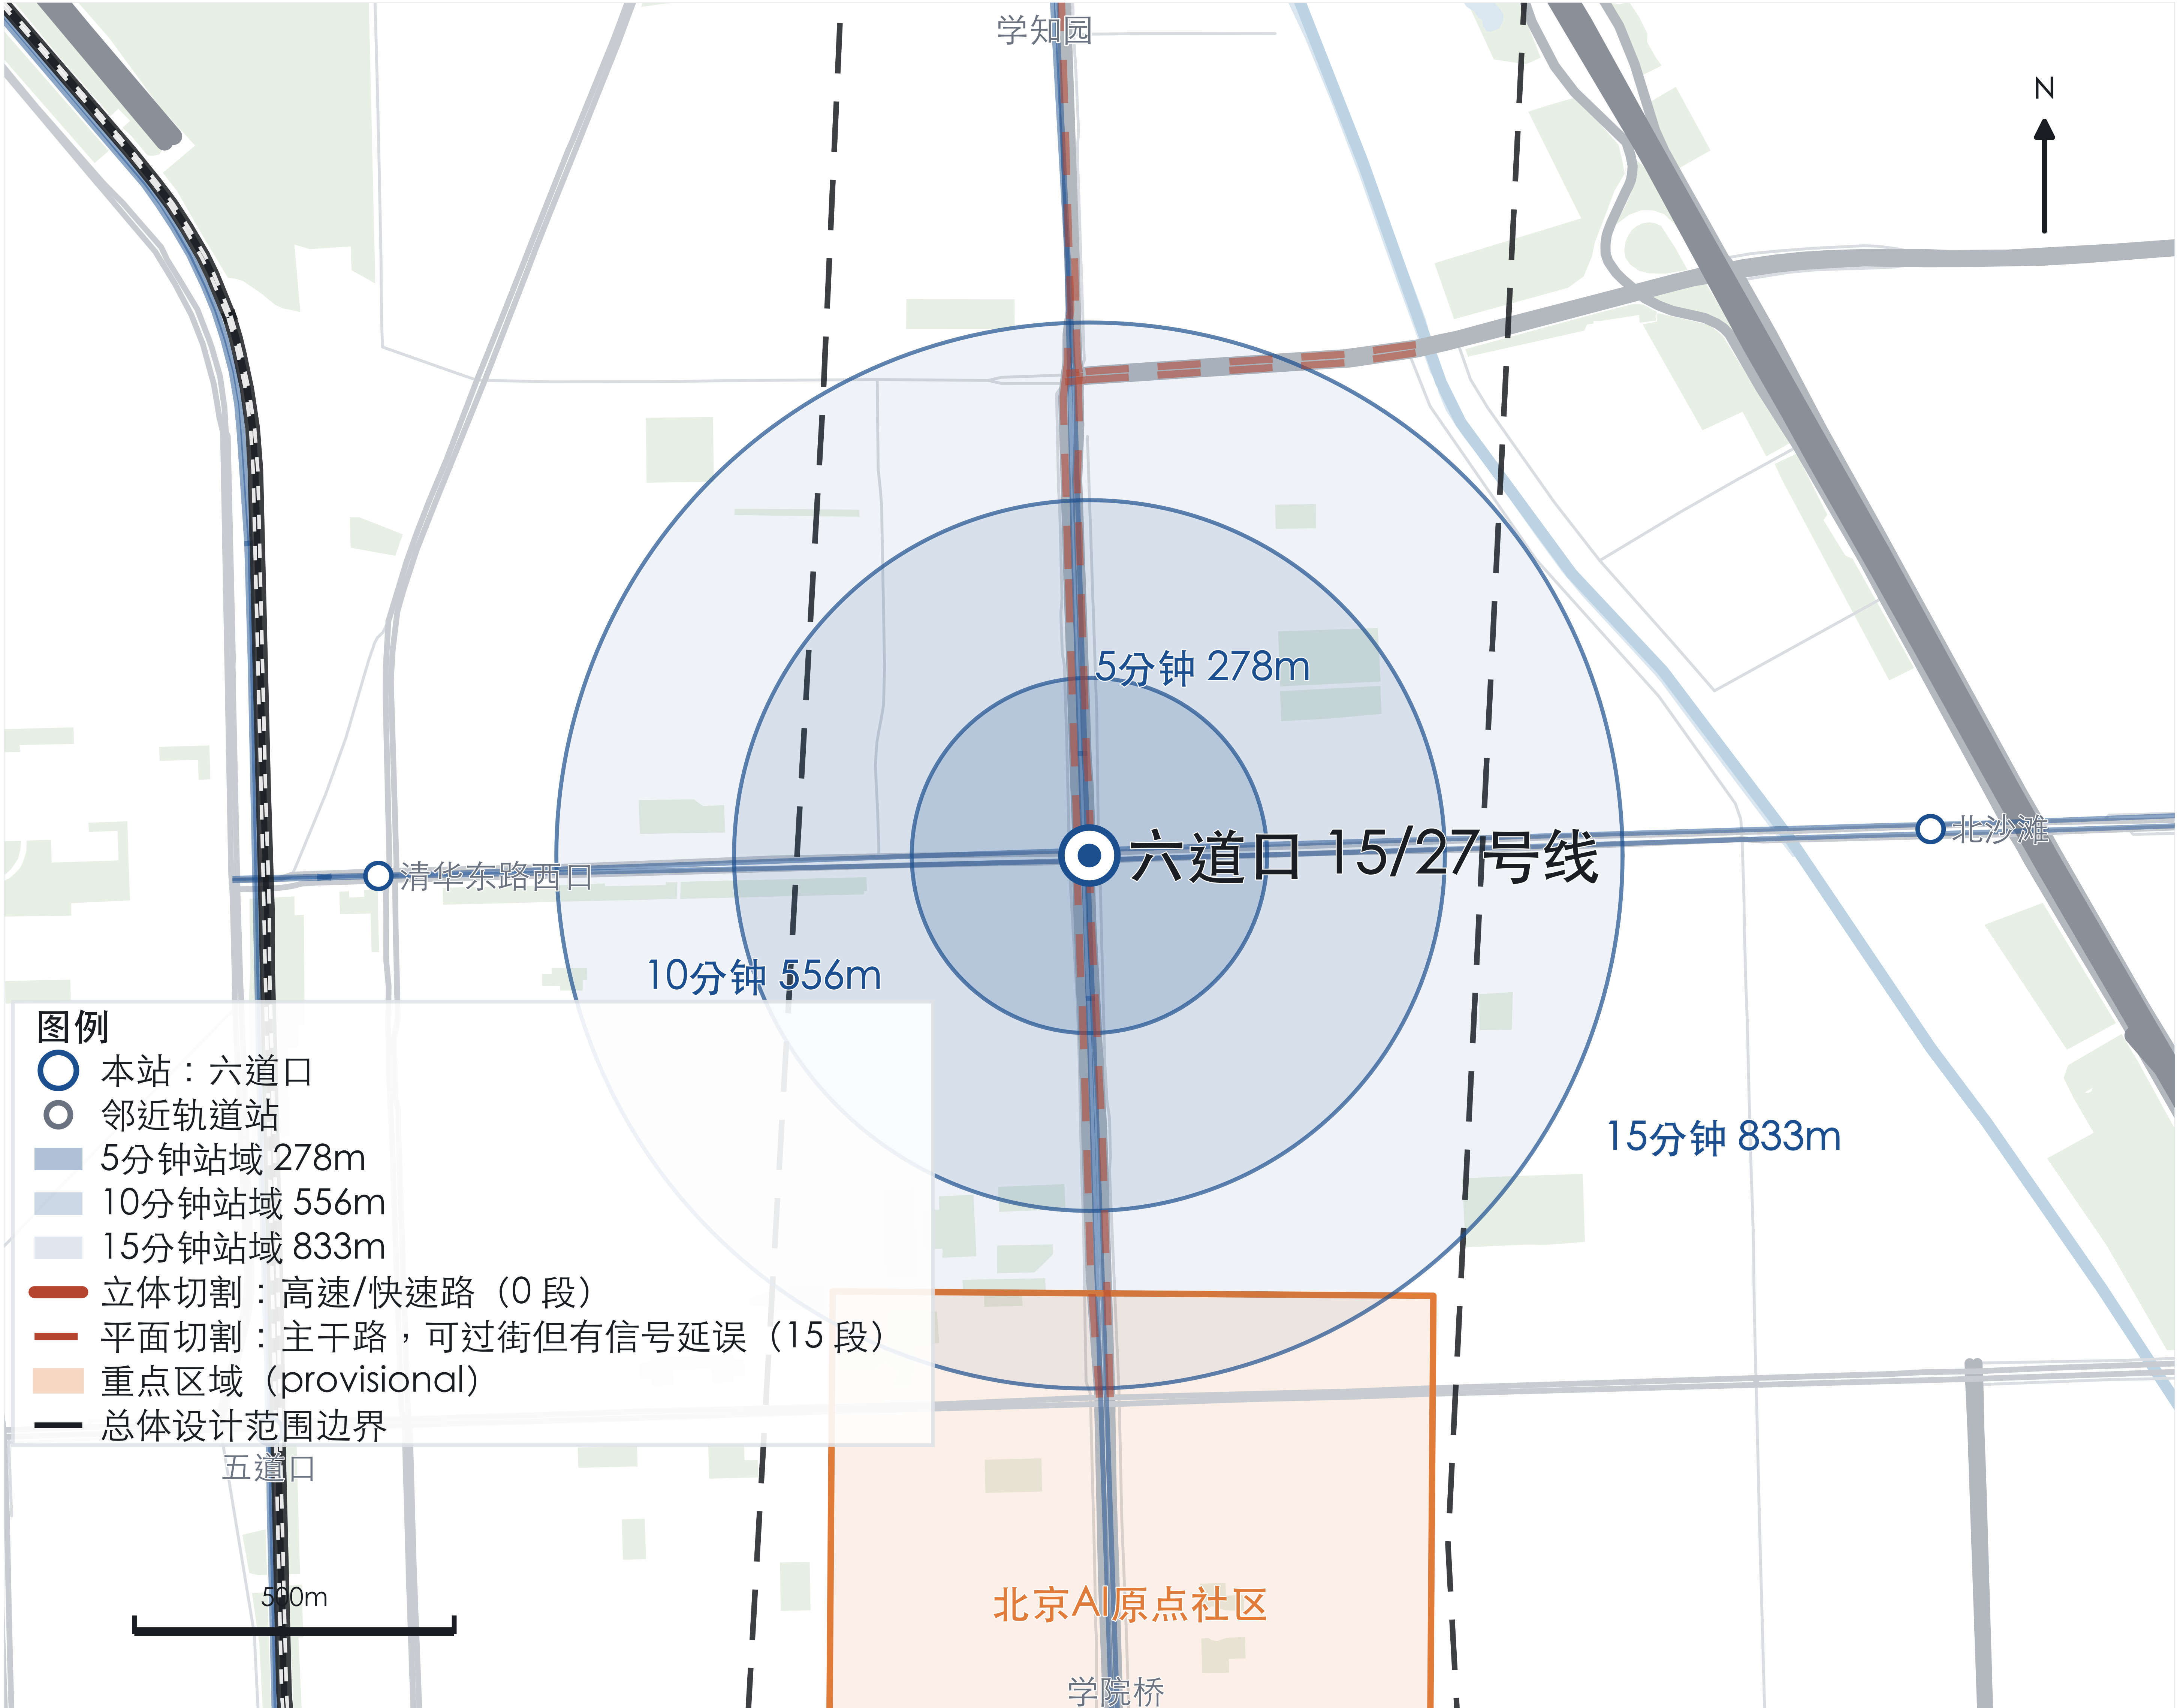

现状诊断

紧邻 AI 原点社区边界（684m）但被学院路主干与校园围墙夹持，过街等待长。

站域口径

站域以车站出入口为原点按步行可达界定，不用车站中心直线半径。半径 = 分钟 × 75 m/min ÷ 1.35 绕行系数，故本站 5 分钟 278m、10 分钟 556m、15 分钟 833m。

切割诊断：立体 0 段 / 平面 15 段

实线为 OSM motorway 与 trunk 等级道路，属立体切割，只能靠桥隧过街，是步行可达的硬断点。虚线为 primary 等级主干路，属平面切割，可过街但受信号周期与路口宽度影响。凡被切割线穿过的圈层为名义可达、实际须绕行或等待，须以实测步行网络与过街点位切除后重算。

待实测

- 过街延误实测
- 校园开放意愿与管理边界
- 非机动车停放缺口

5 分钟核心 · 278m

- 平价餐饮
- 自习与夜间学习
- 便利店与药房
- 非机动车集中停放

10 分钟圈 · 556m

- 学校与社区医疗
- 成果发布与共享会议
- 普通住房更新
- 运动设施

15 分钟圈 · 833m

以既有社区更新为主，不以拆迁换取形式整齐；补齐普通就业、教育医疗与公交接驳，保留小商户与可承受租金。

密度与混合梯度

出入口周边最高、向外递减，功能混合度随距离下降。此处只给相对关系：官方控规与精确边界未发布，容积率与建筑高度保持 unknown，本图不给具体数值。

近期动作

不依赖大拆建、可先行、可回退：


1. 学院路平交口行人相位优先，压缩等待
2. 校园东南角围墙开口接入站口
3. 站口自行车停放正规化，清理占道

站城一体

出入口、公交站台、非机动车停放、人行系统与建筑首层应在同一标高连续贯通，避免出闸后再上下天桥；非机动车在出入口 50m 内集中停放并清理占道。

本图性质

概念设计建议，非法定规划成果。站位为 OpenStreetMap provisional 数据，实测出入口替换后须复算站域与步行圈；边界为仓库 provisional 数据，非官方红线。

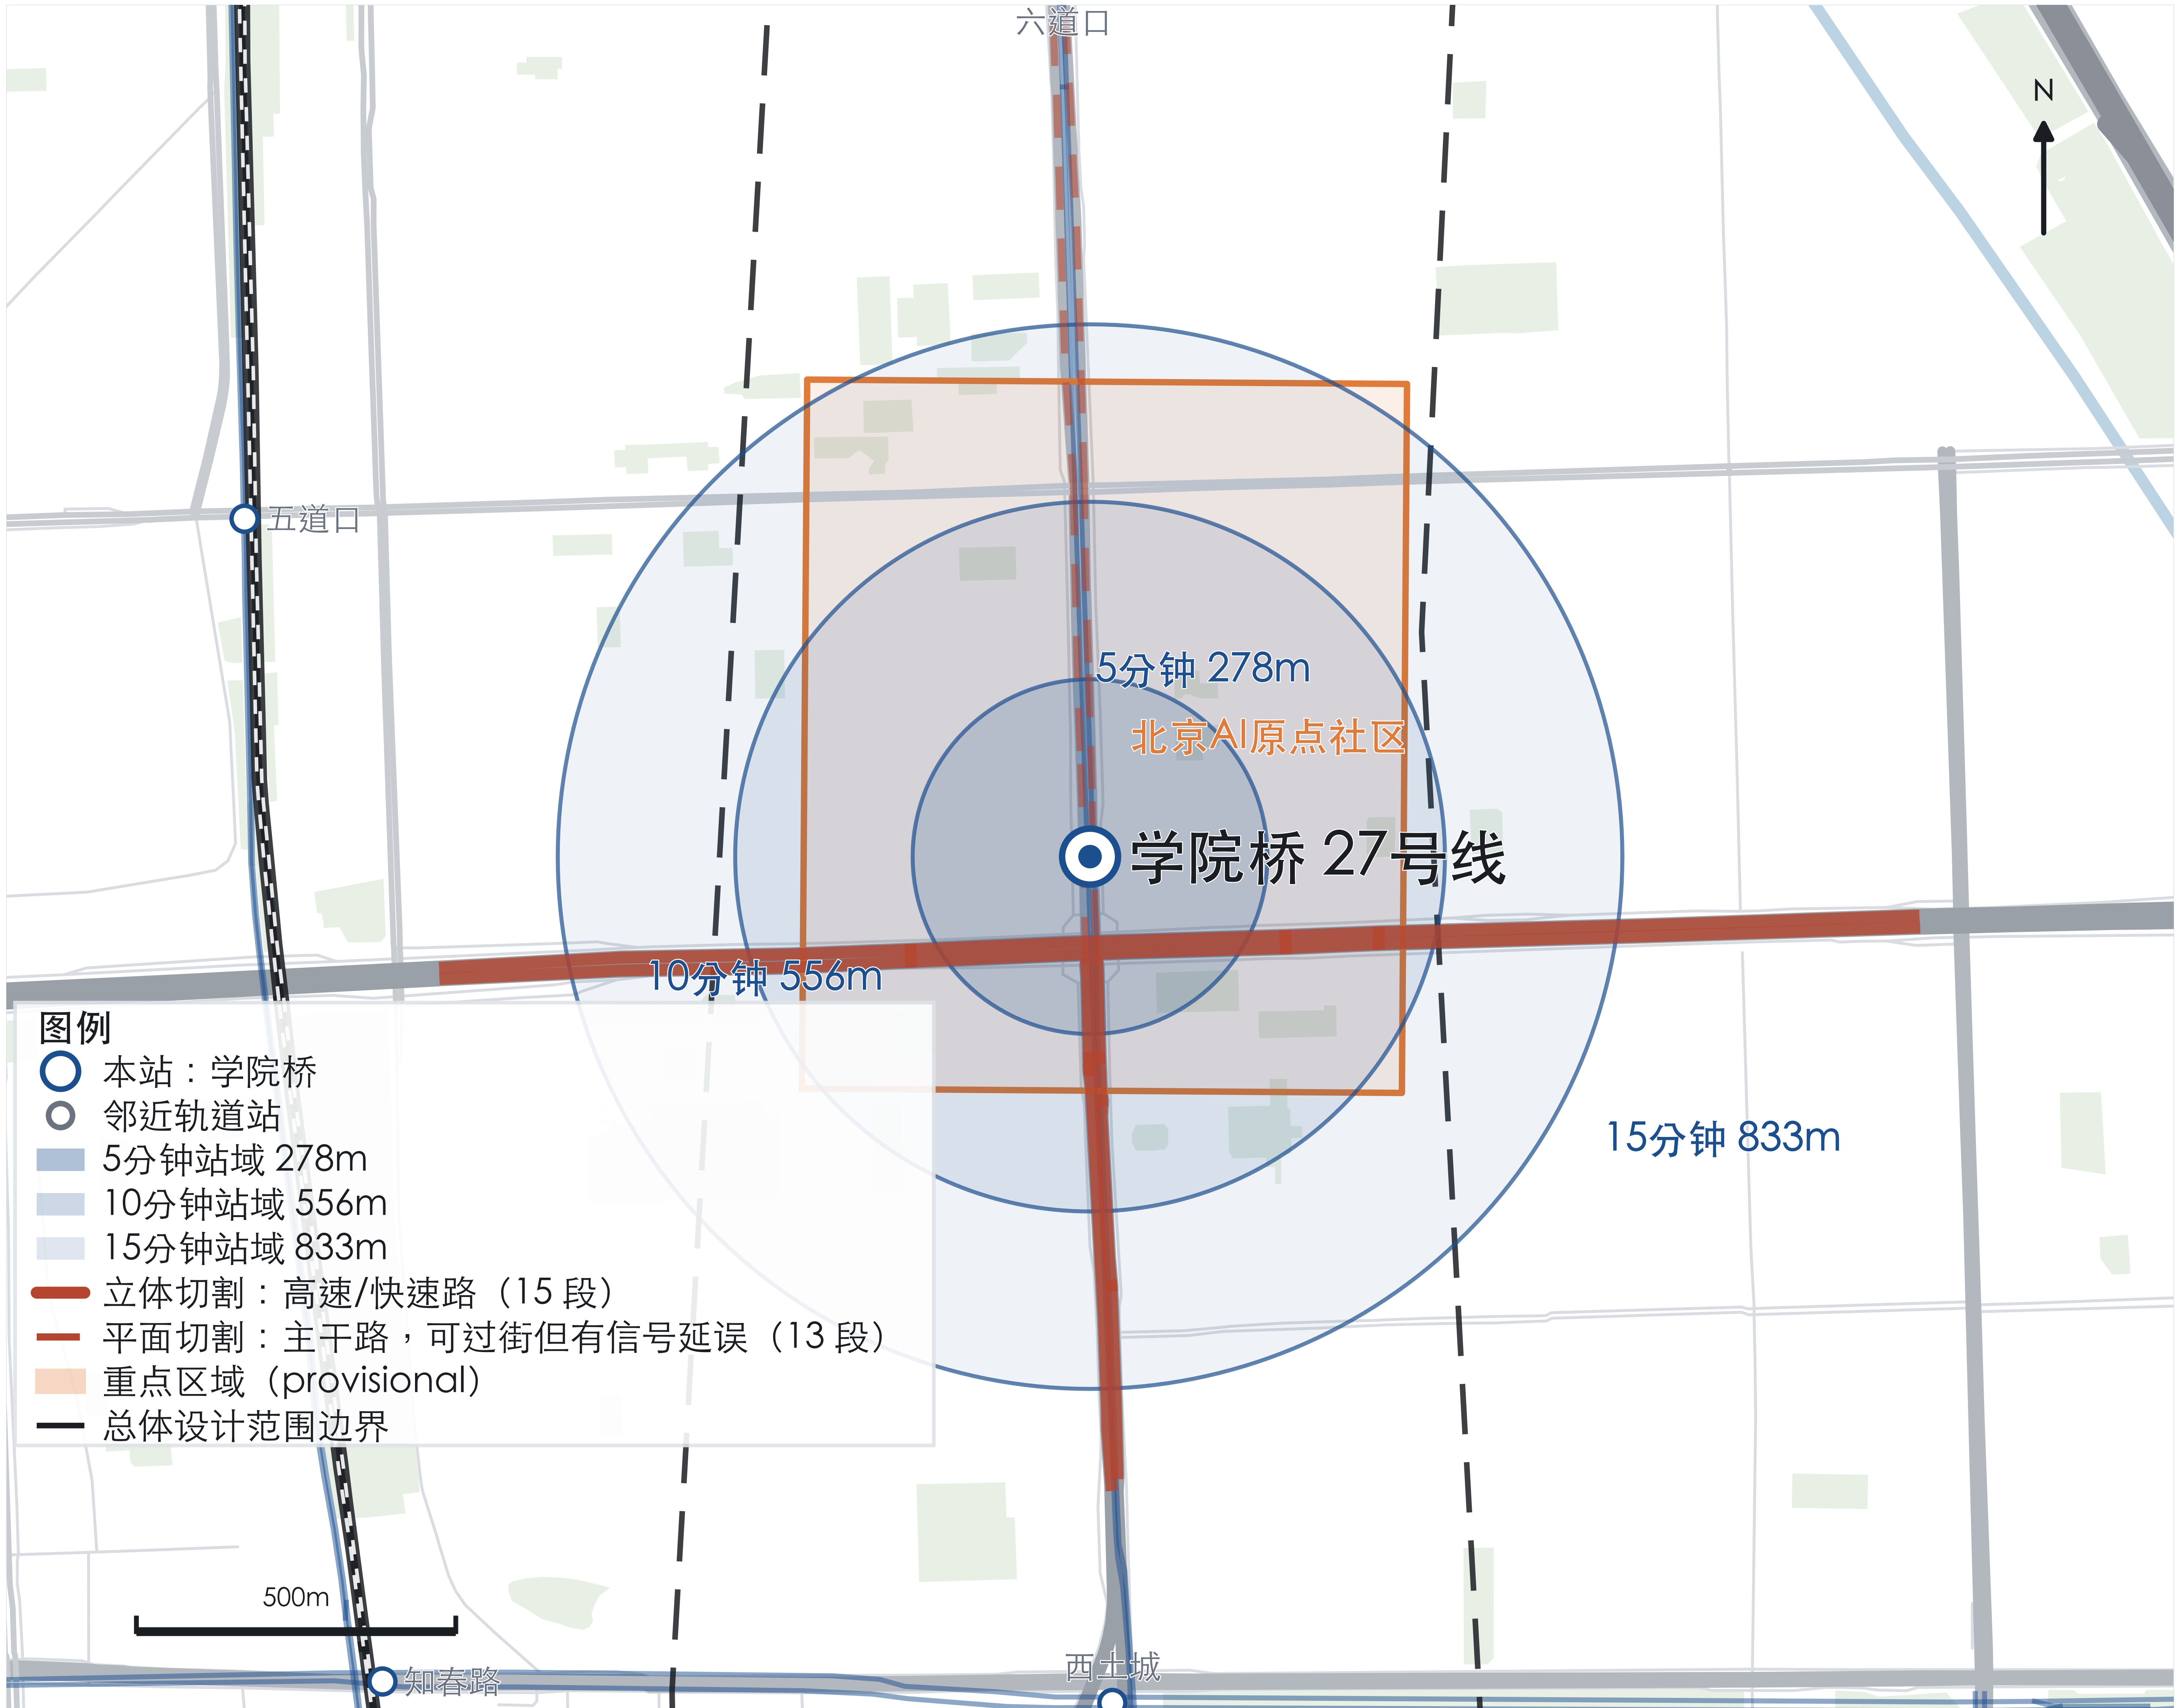

现状诊断

站点落在重点区内，但立交桥区人车混行、导视缺失，桥下空间闲置。

站域口径

站域以车站出入口为原点按步行可达界定，不用车站中心直线半径。半径 = 分钟 × 75 m/min ÷ 1.35 绕行系数，故本站 5 分钟 278m、10 分钟 556m、15 分钟 833m。

切割诊断：立体 15 段 / 平面 13 段

实线为 OSM motorway 与 trunk 等级道路，属立体切割，只能靠桥隧过街，是步行可达的硬断点。虚线为 primary 等级主干路，属平面切割，可过街但受信号周期与路口宽度影响。凡被切割线穿过的圈层为名义可达、实际须绕行或等待，须以实测步行网络与过街点位切除后重算。

待实测

- 桥下空间权属与结构条件
- 夜间照明与安全基线
- 现状容积与拆改留判断

5 分钟核心 · 278m

- 站城复合门厅
- 灵活办公
- 社区服务与托育
- 日常商业首层

10 分钟圈 · 556m

- 综合商场与就业空间
- 医院或社区医疗
- 租赁住房与公寓
- 径向绿廊入口

15 分钟圈 · 833m

以既有社区更新为主，不以拆迁换取形式整齐；补齐普通就业、教育医疗与公交接驳，保留小商户与可承受租金。

密度与混合梯度

出入口周边最高、向外递减，功能混合度随距离下降。此处只给相对关系：官方控规与精确边界未发布，容积率与建筑高度保持 unknown，本图不给具体数值。

近期动作

不依赖大拆建、可先行、可回退：


- 立交桥下空间改造为有照明的步行连廊与公共活动场
- 四向连续过街与统一导视
- 径向绿廊穿透，替代封闭绿带

站城一体

出入口、公交站台、非机动车停放、人行系统与建筑首层应在同一标高连续贯通，避免出闸后再上下天桥；非机动车在出入口 50m 内集中停放并清理占道。

本图性质

概念设计建议，非法定规划成果。站位为 OpenStreetMap provisional 数据，实测出入口替换后须复算站域与步行圈；边界为仓库 provisional 数据，非官方红线。

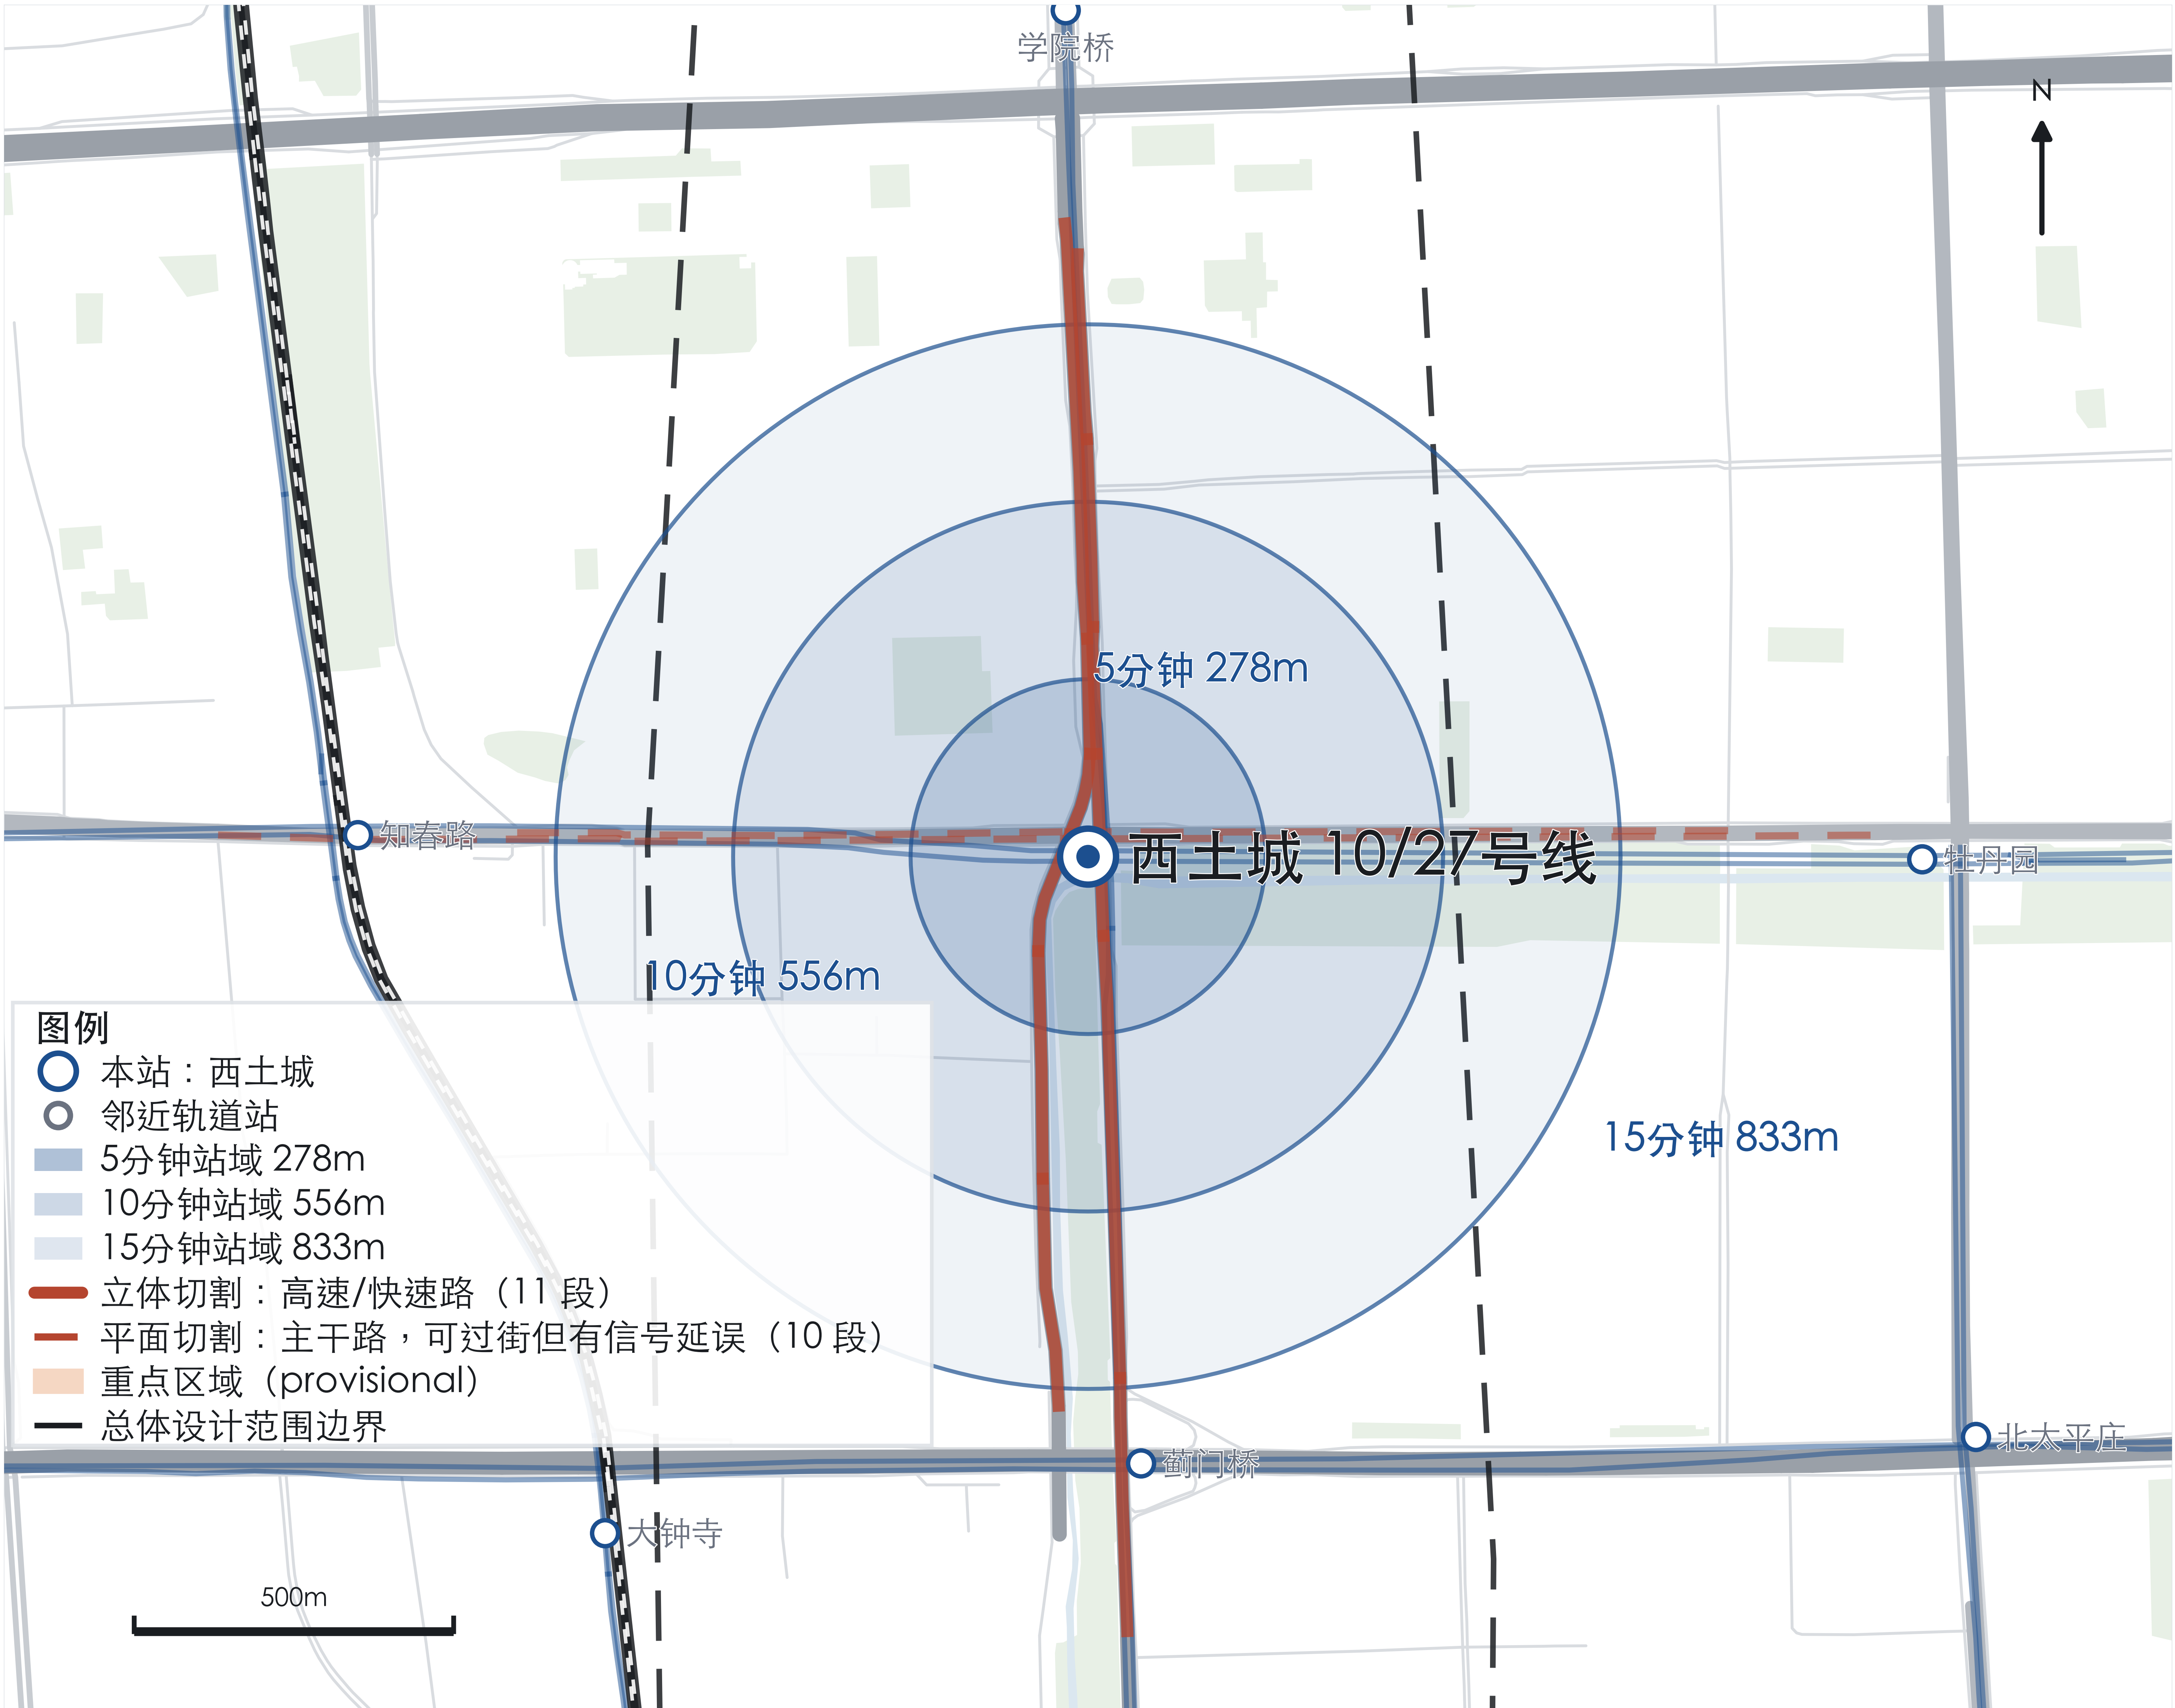

现状诊断

距原点社区 958m，处于两重点区之间的接续段，沿线业态单一、夜间冷清。

站域口径

站域以车站出入口为原点按步行可达界定，不用车站中心直线半径。半径 = 分钟 × 75 m/min ÷ 1.35 绕行系数，故本站 5 分钟 278m、10 分钟 556m、15 分钟 833m。

切割诊断：立体 11 段 / 平面 10 段

实线为 OSM motorway 与 trunk 等级道路，属立体切割，只能靠桥隧过街，是步行可达的硬断点。虚线为 primary 等级主干路，属平面切割，可过街但受信号周期与路口宽度影响。凡被切割线穿过的圈层为名义可达、实际须绕行或等待，须以实测步行网络与过街点位切除后重算。

待实测

- 沿街业态与租金基线
- 夜间人流与安全感调查
- 住房更新意愿

5 分钟核心 · 278m

- 日常商业与餐饮
- 社区服务点
- 共享自习
- 接驳候车

10 分钟圈 · 556m

- 普通住房更新
- 学校与幼托
- 小型运动场地
- 沿街就业空间

15 分钟圈 · 833m

以既有社区更新为主，不以拆迁换取形式整齐；补齐普通就业、教育医疗与公交接驳，保留小商户与可承受租金。

密度与混合梯度

出入口周边最高、向外递减，功能混合度随距离下降。此处只给相对关系：官方控规与精确边界未发布，容积率与建筑高度保持 unknown，本图不给具体数值。

近期动作

不依赖大拆建、可先行、可回退：


1. 沿站步行街段首层业态激活，避免纯办公
2. 补齐夜间照明与连续遮阴
3. 接入南北慢行脊

站城一体

出入口、公交站台、非机动车停放、人行系统与建筑首层应在同一标高连续贯通，避免出闸后再上下天桥；非机动车在出入口 50m 内集中停放并清理占道。

本图性质

概念设计建议，非法定规划成果。站位为 OpenStreetMap provisional 数据，实测出入口替换后须复算站域与步行圈；边界为仓库 provisional 数据，非官方红线。

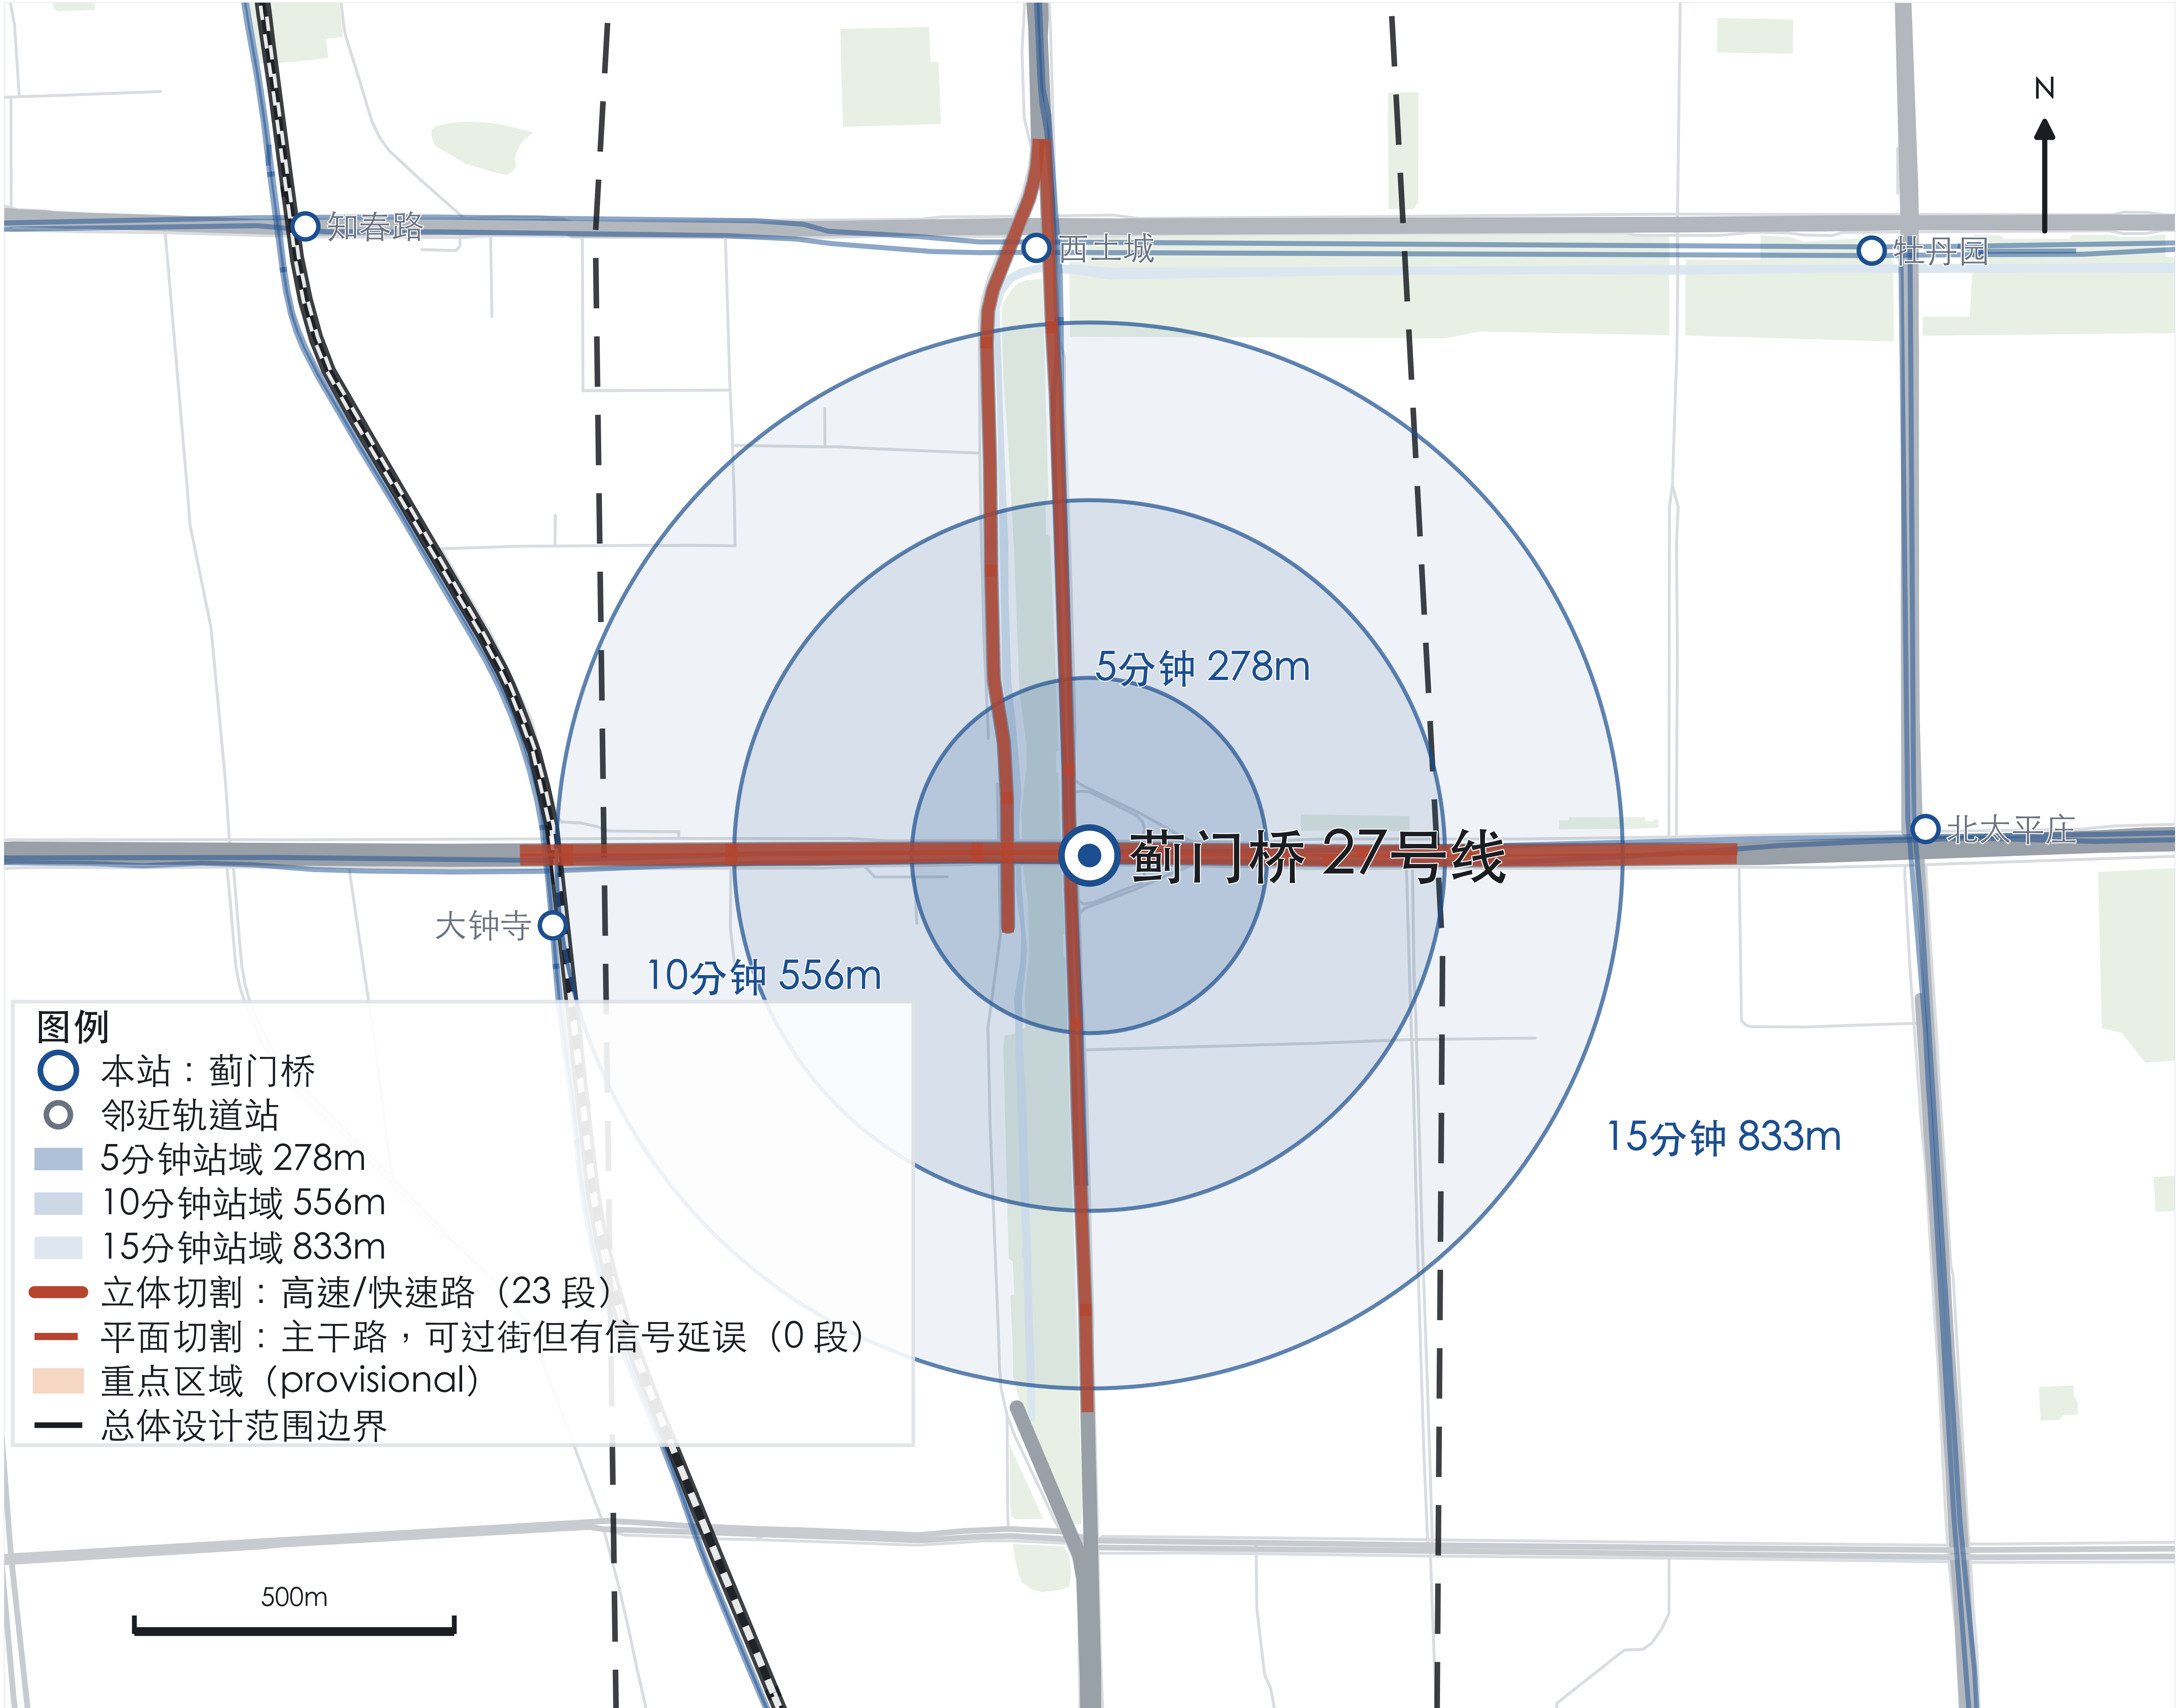

现状诊断

距第三重点区 1.8km，位于慢行脊中段，主干路切断东西向步行联系。

站域口径

站域以车站出入口为原点按步行可达界定，不用车站中心直线半径。半径 = 分钟 × 75 m/min ÷ 1.35 绕行系数，故本站 5 分钟 278m、10 分钟 556m、15 分钟 833m。

切割诊断：立体 23 段 / 平面 0 段

实线为 OSM motorway 与 trunk 等级道路，属立体切割，只能靠桥隧过街，是步行可达的硬断点。虚线为 primary 等级主干路，属平面切割，可过街但受信号周期与路口宽度影响。凡被切割线穿过的圈层为名义可达、实际须绕行或等待，须以实测步行网络与过街点位切除后重算。

待实测

- 东西向步行断点普查
- 绿地可穿透性评估
- 过街需求分布

5 分钟核心 · 278m

- 接驳与便民服务
- 早餐与便利
- 公共休憩
- 非机动车换乘

10 分钟圈 · 556m

- 社区医疗
- 普通住房与就业混合
- 公园入口与运动
- 学校接送空间

15 分钟圈 · 833m

以既有社区更新为主，不以拆迁换取形式整齐；补齐普通就业、教育医疗与公交接驳，保留小商户与可承受租金。

密度与混合梯度

出入口周边最高、向外递减，功能混合度随距离下降。此处只给相对关系：官方控规与精确边界未发布，容积率与建筑高度保持 unknown，本图不给具体数值。

近期动作

不依赖大拆建、可先行、可回退：


1. 东西向过街加密，缩短绕行
2. 绿脊在此段连通，不做封闭隔离带
3. 站口公共休憩与遮阴

站城一体

出入口、公交站台、非机动车停放、人行系统与建筑首层应在同一标高连续贯通，避免出闸后再上下天桥；非机动车在出入口 50m 内集中停放并清理占道。

本图性质

概念设计建议，非法定规划成果。站位为 OpenStreetMap provisional 数据，实测出入口替换后须复算站域与步行圈；边界为仓库 provisional 数据，非官方红线。

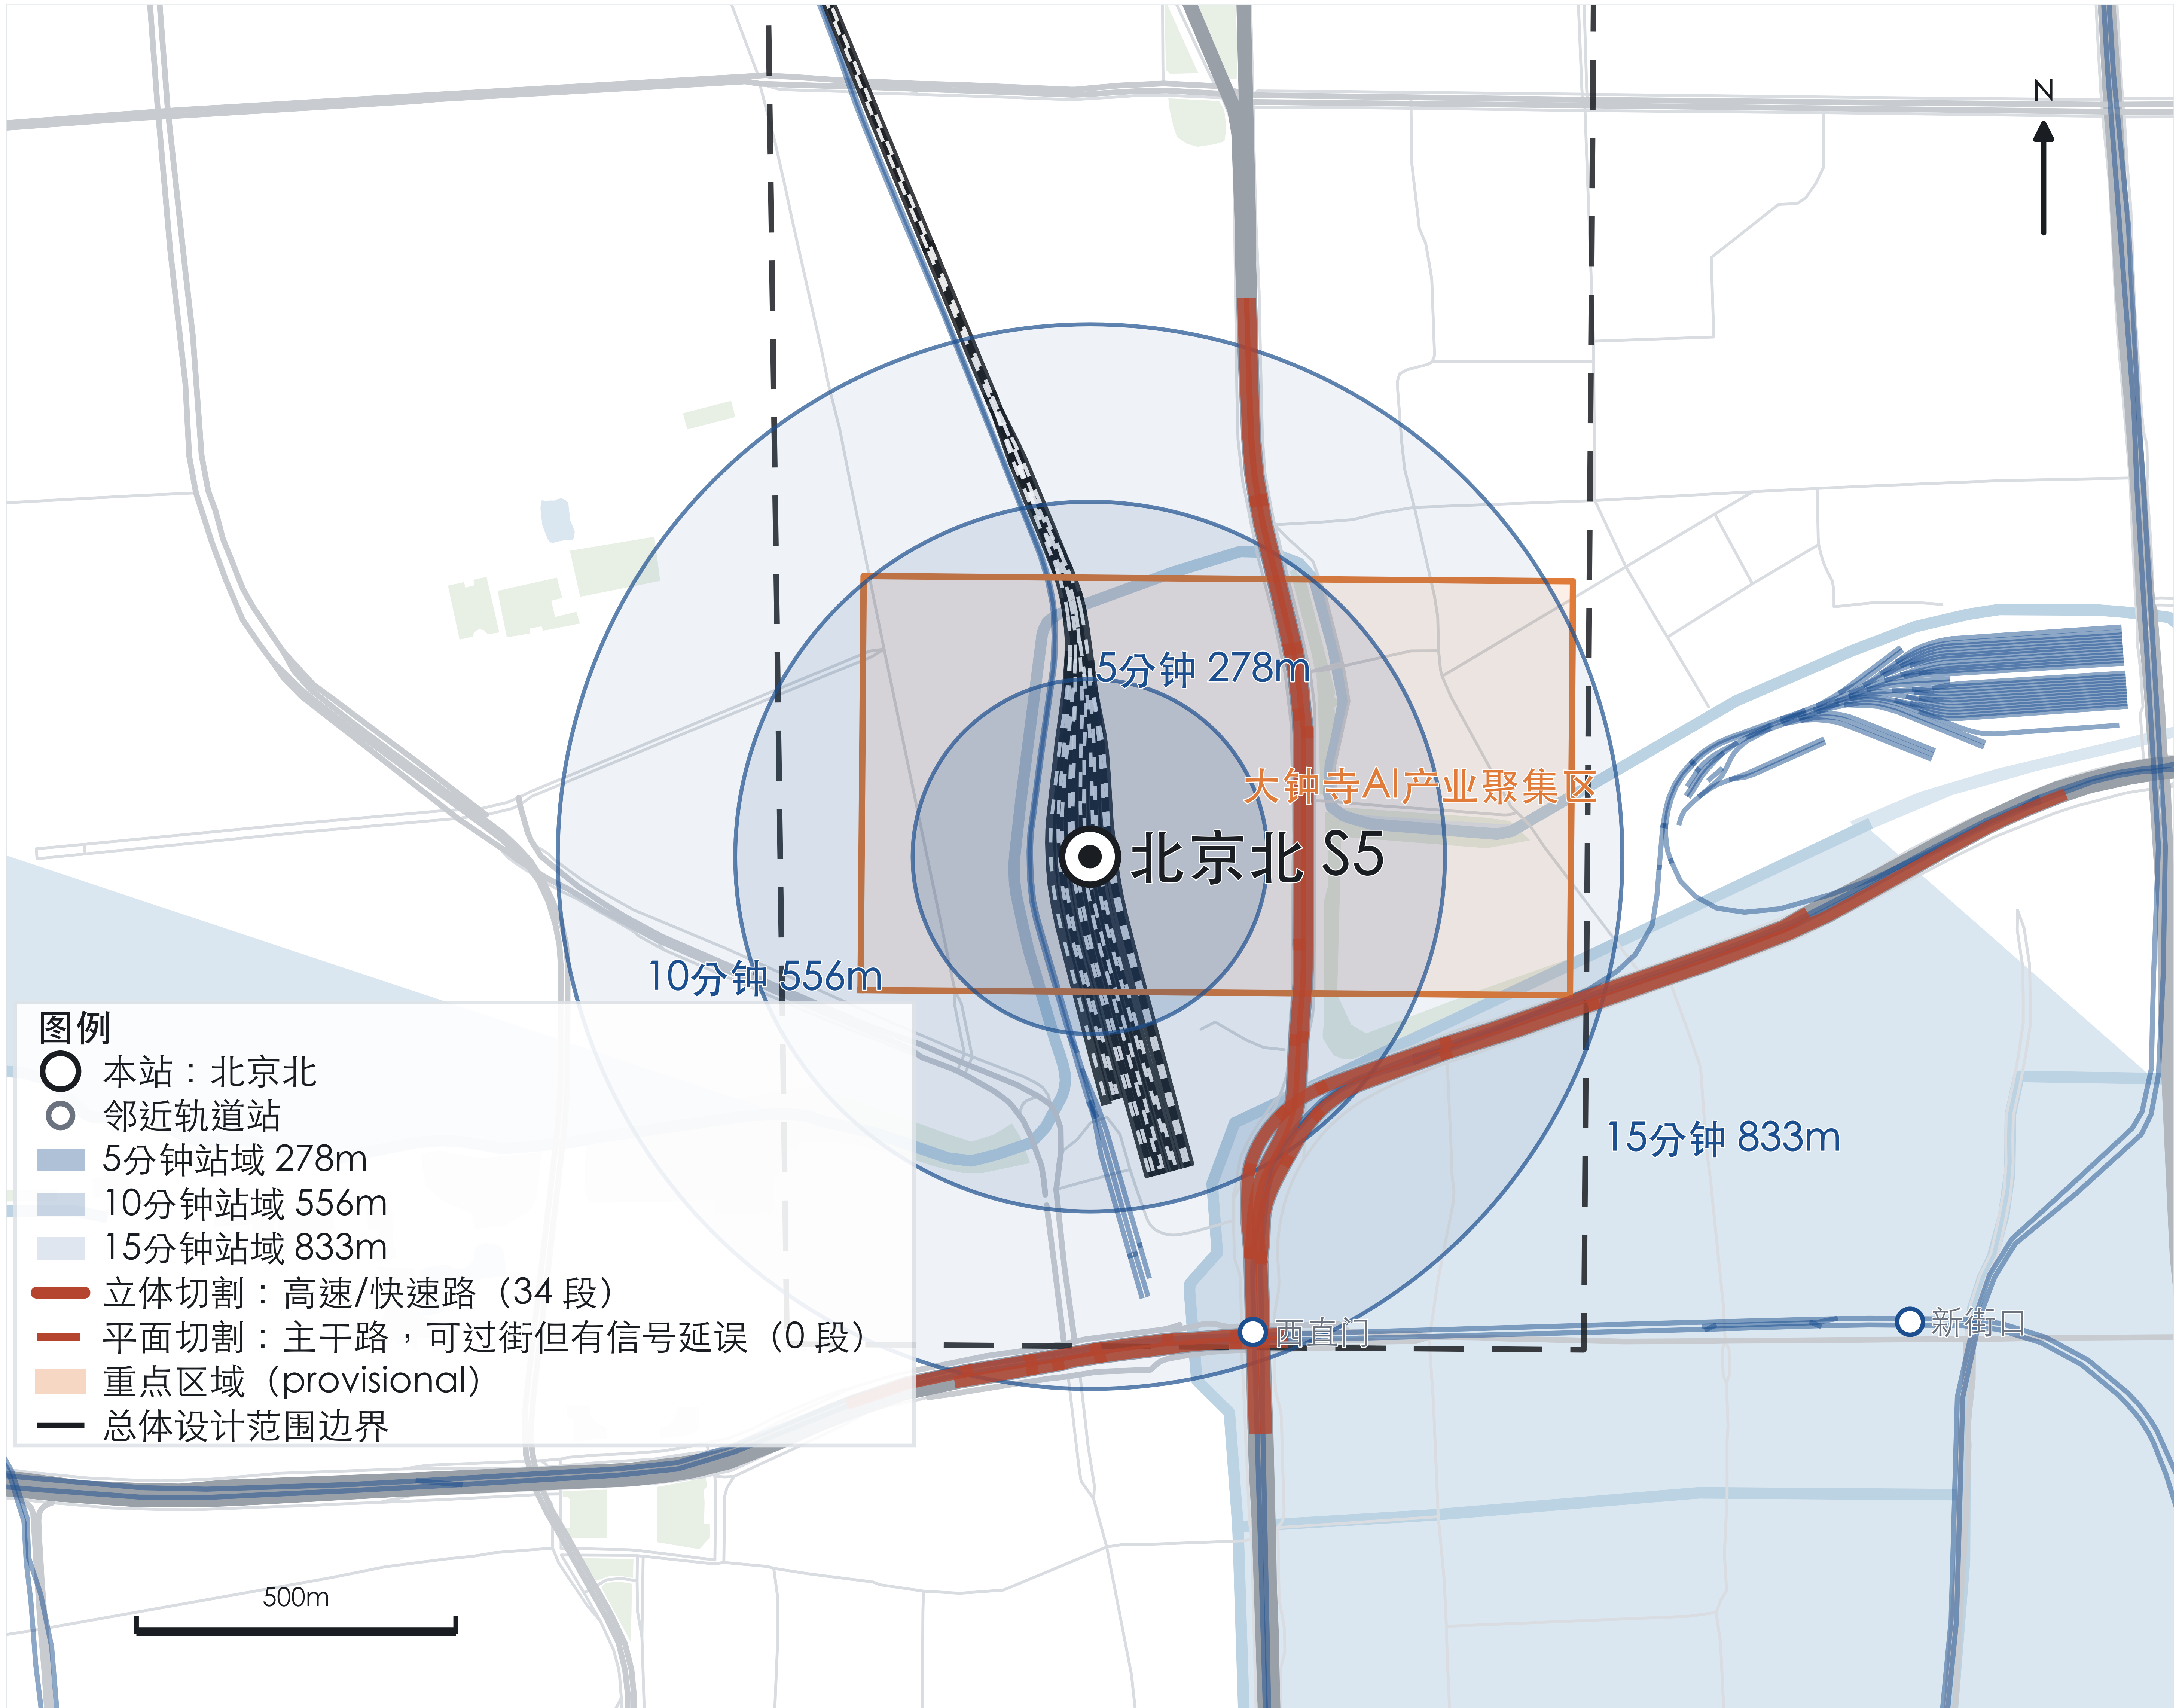

现状诊断

位于第三重点区临时 polygon 内，是市郊铁路而非地铁站；与西直门地铁换乘步行距离长、指引弱。

站域口径

站域以车站出入口为原点按步行可达界定，不用车站中心直线半径。半径 = 分钟 × 75 m/min ÷ 1.35 绕行系数，故本站 5 分钟 278m、10 分钟 556m、15 分钟 833m。

切割诊断：立体 34 段 / 平面 0 段

实线为 OSM motorway 与 trunk 等级道路，属立体切割，只能靠桥隧过街，是步行可达的硬断点。虚线为 primary 等级主干路，属平面切割，可过街但受信号周期与路口宽度影响。凡被切割线穿过的圈层为名义可达、实际须绕行或等待，须以实测步行网络与过街点位切除后重算。

待实测

- 换乘步行时间与迷路点实测
- 铁路用地权属与文保控制线
- 站前交通组织

5 分钟核心 · 278m

- 铁路遗产门厅与文化展示
- 全时商业与餐饮
- 换乘导视枢纽
- 行李友好动线

10 分钟圈 · 556m

- 公共服务与国际交往
- 租赁住房
- 灵活办公
- 遗址公园入口

15 分钟圈 · 833m

以既有社区更新为主，不以拆迁换取形式整齐；补齐普通就业、教育医疗与公交接驳，保留小商户与可承受租金。

密度与混合梯度

出入口周边最高、向外递减，功能混合度随距离下降。此处只给相对关系：官方控规与精确边界未发布，容积率与建筑高度保持 unknown，本图不给具体数值。

近期动作

不依赖大拆建、可先行、可回退：


1. 北京北—西直门换乘通道连续化与统一导视
2. 京张遗址公园在此设主入口
3. 站前广场机动车与步行分离

站城一体

出入口、公交站台、非机动车停放、人行系统与建筑首层应在同一标高连续贯通，避免出闸后再上下天桥；非机动车在出入口 50m 内集中停放并清理占道。

本图性质

概念设计建议，非法定规划成果。站位为 OpenStreetMap provisional 数据，实测出入口替换后须复算站域与步行圈；边界为仓库 provisional 数据，非官方红线。

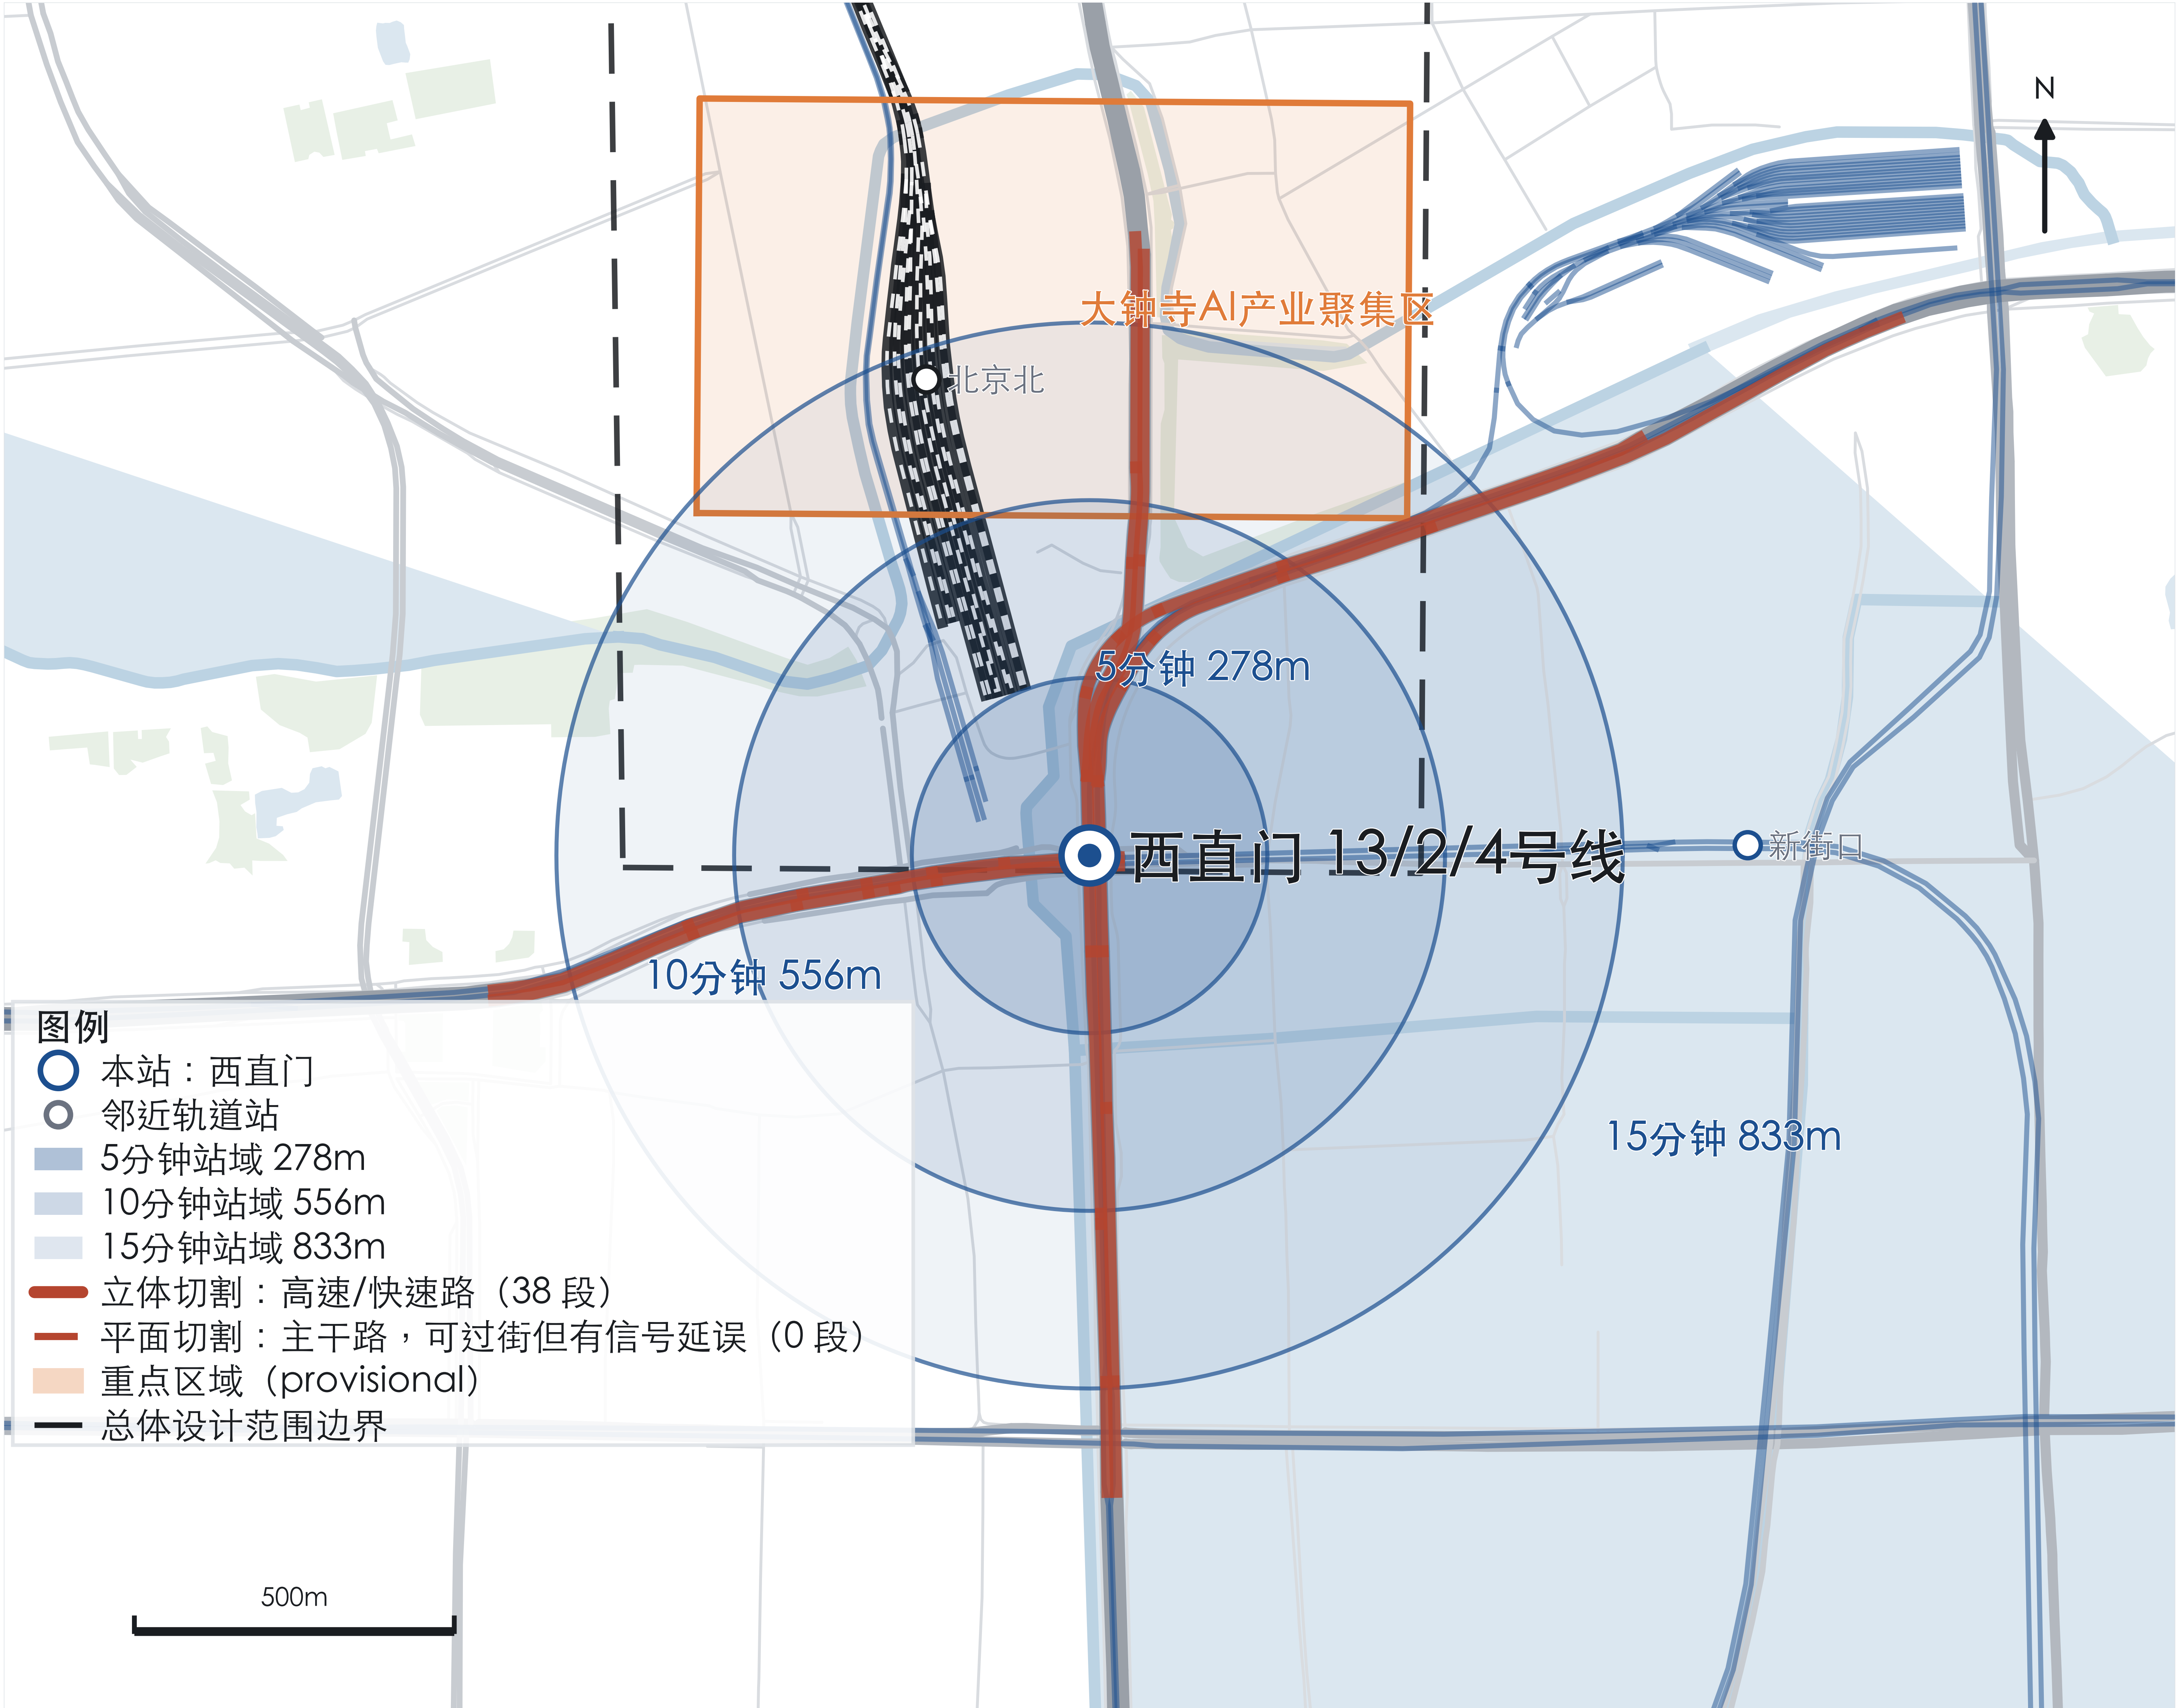

现状诊断

三线换乘且紧邻研究范围南界，站域被西直门外大街与立交切割，属高强度既有建成区。

站域口径

站域以车站出入口为原点按步行可达界定，不用车站中心直线半径。半径 = 分钟 × 75 m/min ÷ 1.35 绕行系数，故本站 5 分钟 278m、10 分钟 556m、15 分钟 833m。

切割诊断：立体 38 段 / 平面 0 段

实线为 OSM motorway 与 trunk 等级道路，属立体切割，只能靠桥隧过街，是步行可达的硬断点。虚线为 primary 等级主干路，属平面切割，可过街但受信号周期与路口宽度影响。凡被切割线穿过的圈层为名义可达、实际须绕行或等待，须以实测步行网络与过街点位切除后重算。

待实测

- 三线换乘客流与瓶颈
- 既有社区更新意愿与租金承受力
- 小商户经营现状

5 分钟核心 · 278m

- 三线换乘优化
- 全时商业
- 公共服务窗口
- 夜间照明与安全

10 分钟圈 · 556m

- 普通就业岗位
- 既有社区更新
- 医疗与教育补齐
- 非机动车与公交接驳

15 分钟圈 · 833m

以既有社区更新为主，不以拆迁换取形式整齐；补齐普通就业、教育医疗与公交接驳，保留小商户与可承受租金。

密度与混合梯度

出入口周边最高、向外递减，功能混合度随距离下降。此处只给相对关系：官方控规与精确边界未发布，容积率与建筑高度保持 unknown，本图不给具体数值。

近期动作

不依赖大拆建、可先行、可回退：

1. 换乘导视与步行连续性优先，不做大拆大建
2. 西直门外大街过街与非机动车路权改善
3. 既有社区以更新为主，保留小商户


站城一体

出入口、公交站台、非机动车停放、人行系统与建筑首层应在同一标高连续贯通，避免出闸后再上下天桥；非机动车在出入口 50m 内集中停放并清理占道。

本图性质

概念设计建议，非法定规划成果。站位为 OpenStreetMap provisional 数据，实测出入口替换后须复算站域与步行圈；边界为仓库 provisional 数据，非官方红线。

众智园AI自主创新加速区

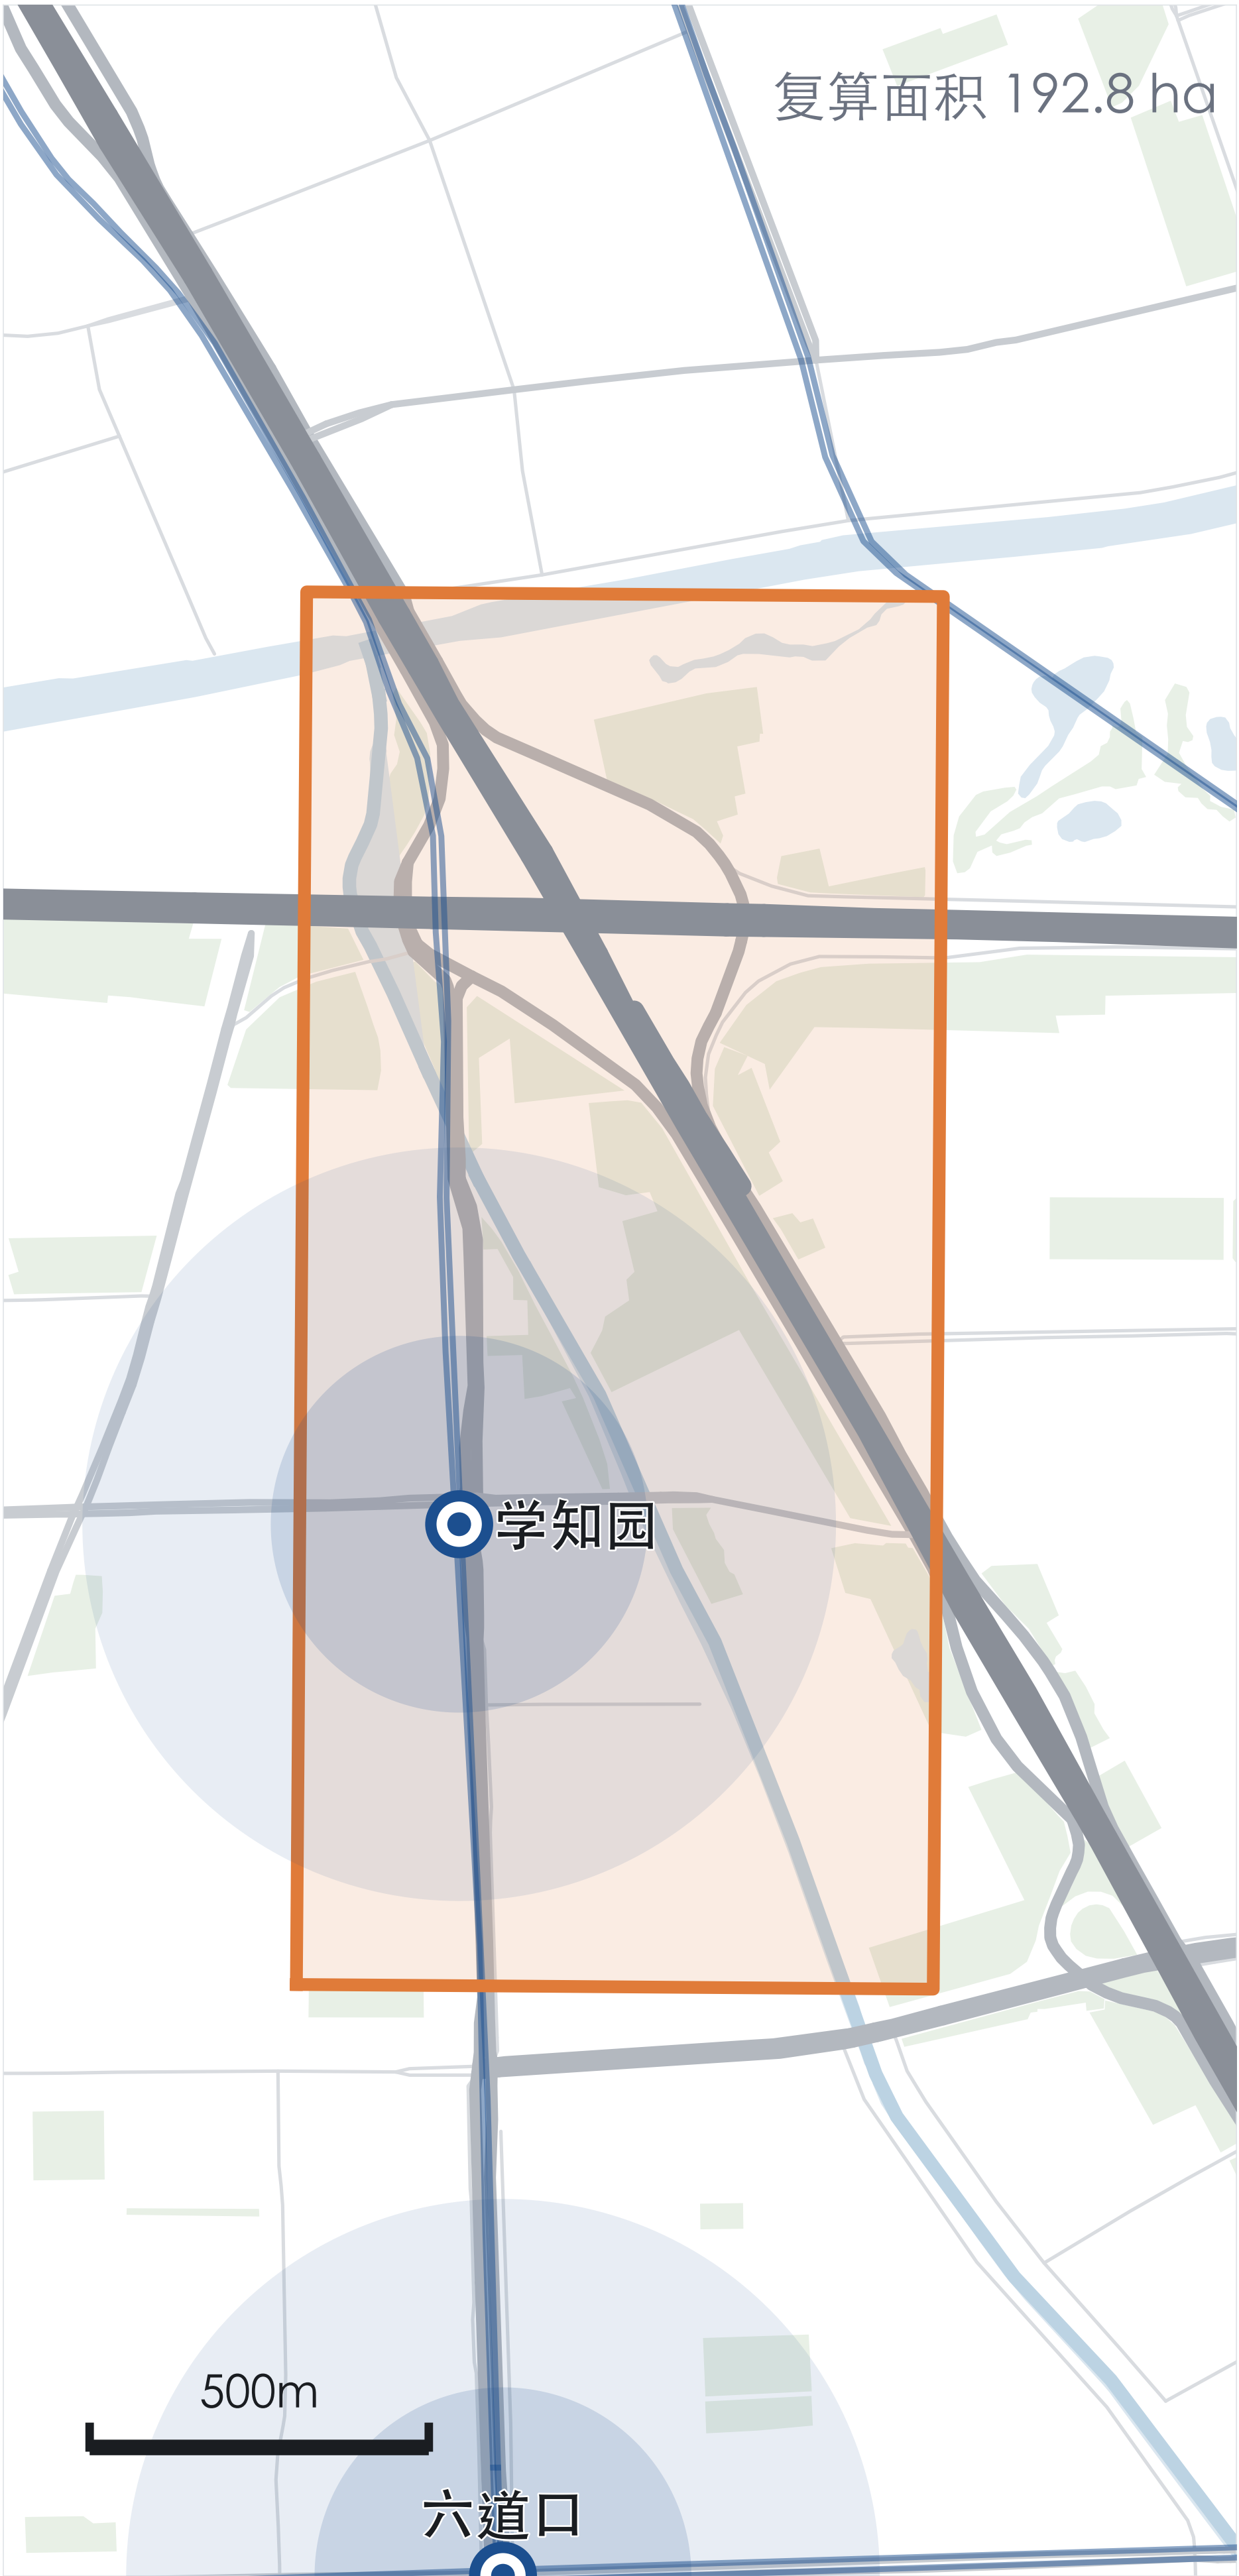

北京AI原点社区



大钟寺AI产业聚集区



数据校核：大钟寺重点区 polygon 与真实站位偏差



分期与实施顺序

近期（可先行、低成本、可回退）

- 站口 200m 内连续步道、雨棚、照明与无障碍改造（7站同步）
- 平交口行人相位优先与过街加密，先做学院路、西直门外大街
- 非机动车停放正规化，清理站口占道
- 统一导视：北京北—西直门换乘通道优先

中期（需专项论证）

- 跨京藏高速、跨铁路慢行 connector（学知园、六道口）
- 学院桥立交桥下空间改造为步行连廊与公共活动场
- 园区与校园围墙开口，站到园/站到校直连
- 10分钟圈补齐社区医疗、托育、学校与运动设施

远期（需控规与权属落实）

- 站城复合核心的功能混合与租赁住房供给
- 京张遗址公园主入口与遗产门厅（北京北）
- 径向绿廊穿透，形成连通而非封闭的绿环
- 既有社区以更新为主，保留小商户与可承受租金

尚未解决 / 需业主与官方数据决定

- 范围口径已定：按官方四至（业主 2026-08-08 确认），上地、清河、西二旗不出逐站详图
- PROV-KEY-003 大钟寺 polygon 偏差约 2192m，须以官方重点区边界复核
- 官方红线、控规指标、道路红线、权属、文保控制线均未发布
- 站位为 OpenStreetMap provisional 数据，实测出入口发布后 9 张图板须整体复算